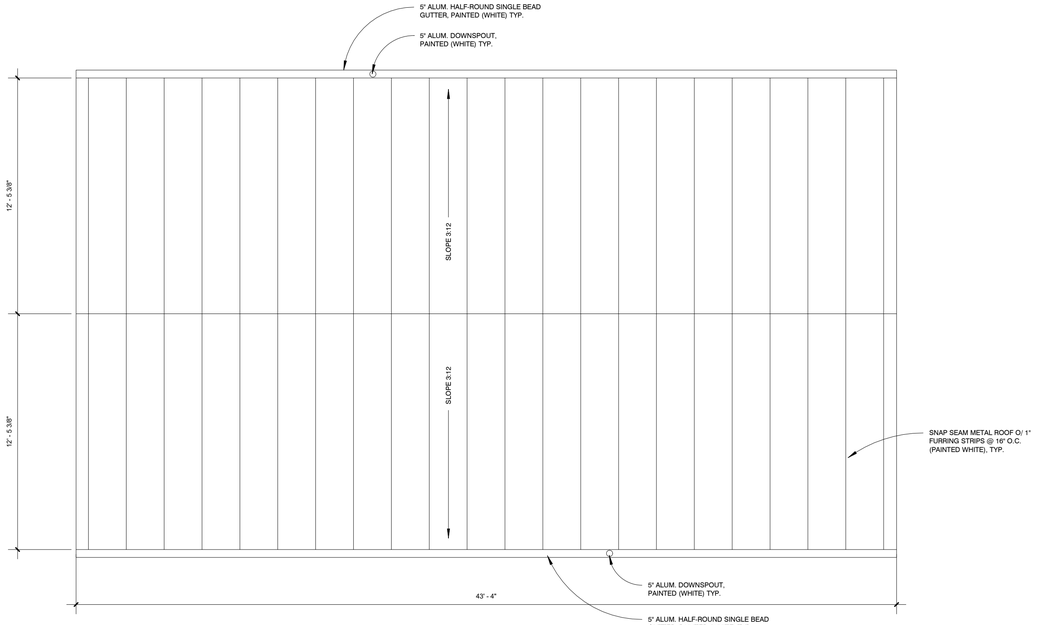

1 ROOF
1/4" = 1'-0"

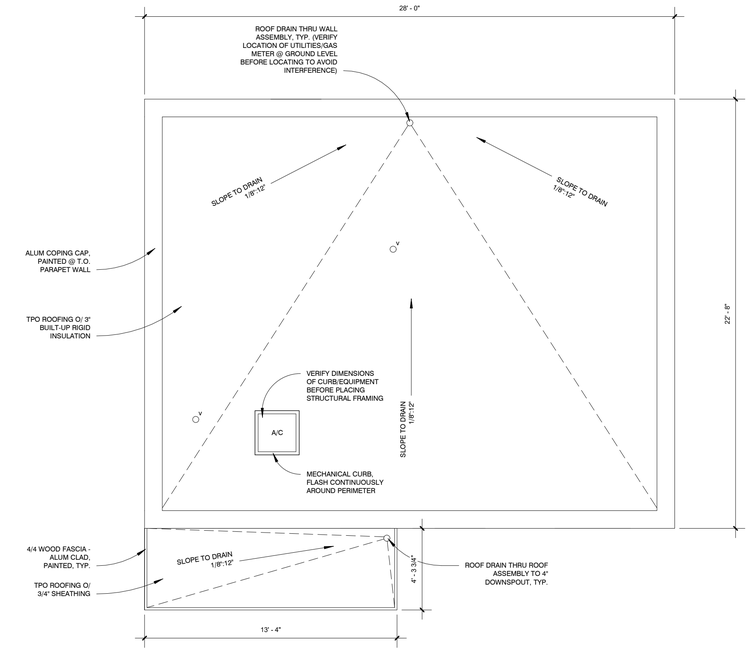

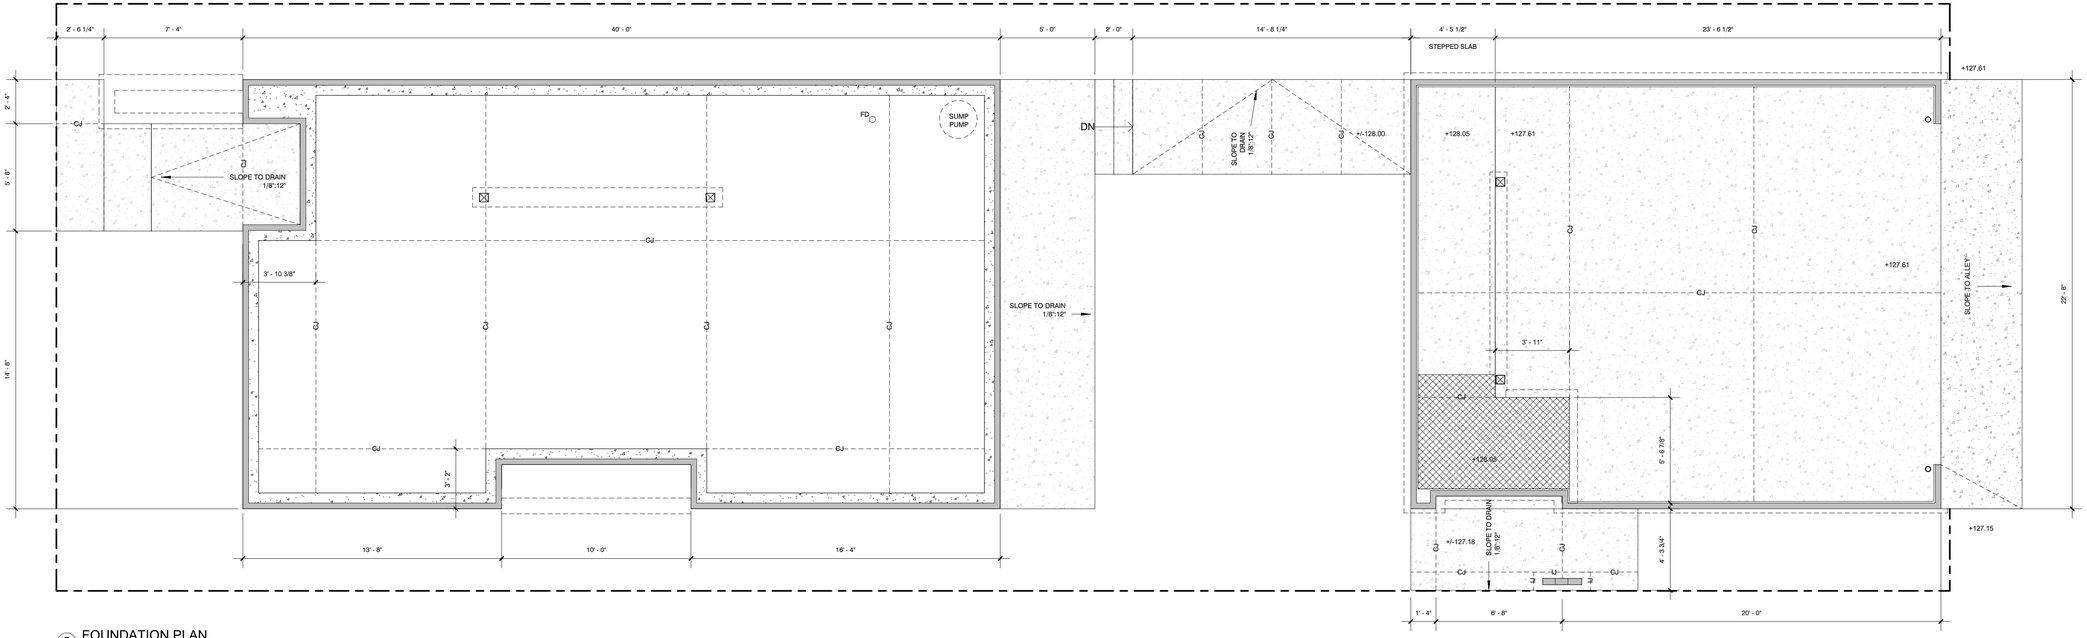

2 FOUNDATION PLAN
1/4" = 1'-0"

GENERAL NOTES

1) SOIL BEARING PRESSURE PER SOILS REPORT INDICATES 2,000 LBS/S.F. BELOW A DEPTH OF 3'-6" @ HOUSE AND 3'-10" @ GARAGE. ALL FOOTINGS SHALL CONFORM TO SOILS REPORT RECOMMENDATIONS (SEE REPORT FOR SPECIFICATIONS).

2) PROVIDE BACK-FLOW PREVENTER ON SEWAGE LINE

3) PROVIDE SHUT-OFF VALVE FOR WEATHERIZING OF HOSE BIBS

4) PLUMBER TO VERIFY ACCURACY OF ALL NOTATED SLAB PENETRATION DIMENSIONS FOR PLUMBING LOCATIONS BEFORE INSTALLATION.

5) ALL SLAB PENETRATIONS AND UNDERGROUND COMPONENTS SHALL BE VERIFIED BEFORE CONCRETE POUR.

ROOF & FOUNDATION LEGEND

	INSULATED CONCRETE SLAB (WHERE INDICATED	1.5"D	SINK DRAIN ROUGH-IN	W	WATER SUPPLY ROUGH-IN
	CONCRETE SLAB (PER STRUCTURE)	3"D	SEWAGE DRAIN ROUGH-IN	V	VENT STACK / EXHAUST
		FD	FLOOR DRAIN	HB	HOSE BIB
		G	GAS CONNECTION		4" DOWNSPOUT

bioLINIA, LLC.

2060 WABASH ST.
DETROIT, MI 48216
www.bioLINIA.com

1588 ELM RESIDENCE

1588 ELM, DETROIT, MI 48216

DEVELOPER

BALLET REAL ESTATE
1701 Trumbull Ave. #5
Detroit, MI 48216
Phone: (415) 279 0953

Brian Mulloy - OWNER

DESIGNER

bioLINIA LLC
2060 Wabash St.
Detroit, MI 48216
Phone: (313) 330 2443
Email: becky@bioLINIA.com

Becky Nix, LEED(AP) - PRINCIPAL IN CHARGE

STRUCTURAL ENGINEER

LM ENGINEERING
25315 Dequindre Rd.
Madison Heights, MI 48071
Phone: (248) 672 1895
Email: Lawrence@LM-Engineering.net

Lawrence Mangindin - ENGINEER

GENERAL CONTRACTOR

ARTISAN CONTRACTING LLC
535 Griswold St. STE 111-195
Detroit, MI 48226
Phone: (313) 909 0477
Email: shoverbey@gmail.com

Shane Overbey - Builder License #2101207828

PERMIT SET

No.	Description	Date

ROOF & FOUNDATION PLANS

Project number	2019_1588
Date	11/30/2020
Drawn by	BN
Checked by	BN
Scale	1/4" = 1'-0"

A0.01

12/3/2020 2:28:27 PM