

1588 ELM, DETROIT, MI 48216

BALLET REAL ESTATE
1701 Trumbull Ave. #5
Detroit, MI 48216
Phone: (415) 279 0953

Brian Mulloy - OWNER

bioLINIA LLC
2060 Wabash St.
Detroit, MI 48216
Phone: (313) 330 2443
Email: becky@bioLINIA.com

Becky Nix, LEED(AP) - PRINCIPAL IN CHARGE

LM ENGINEERING
25315 Dequindre Rd.
Madison Heights, MI 48071
Phone: (248) 672 1895
Email: Lawrence@LM-Engineering.net

Lawrence Mangindin - ENGINEER


ARTISAN CONTRACTING LLC
535 Griswold St. STE 111-195
Detroit, MI 48226
Phone: (313) 909 0477
Email: shoverbey@gmail.com

Shane Overbey - Builder License #2101207828


[illegible]

Project number	2019_1588
Date	11/30/2020
Drawn by	BN
Checked by	BN
Scale	1/4" = 1'-0"

12/3/2020 2:29:35 PM

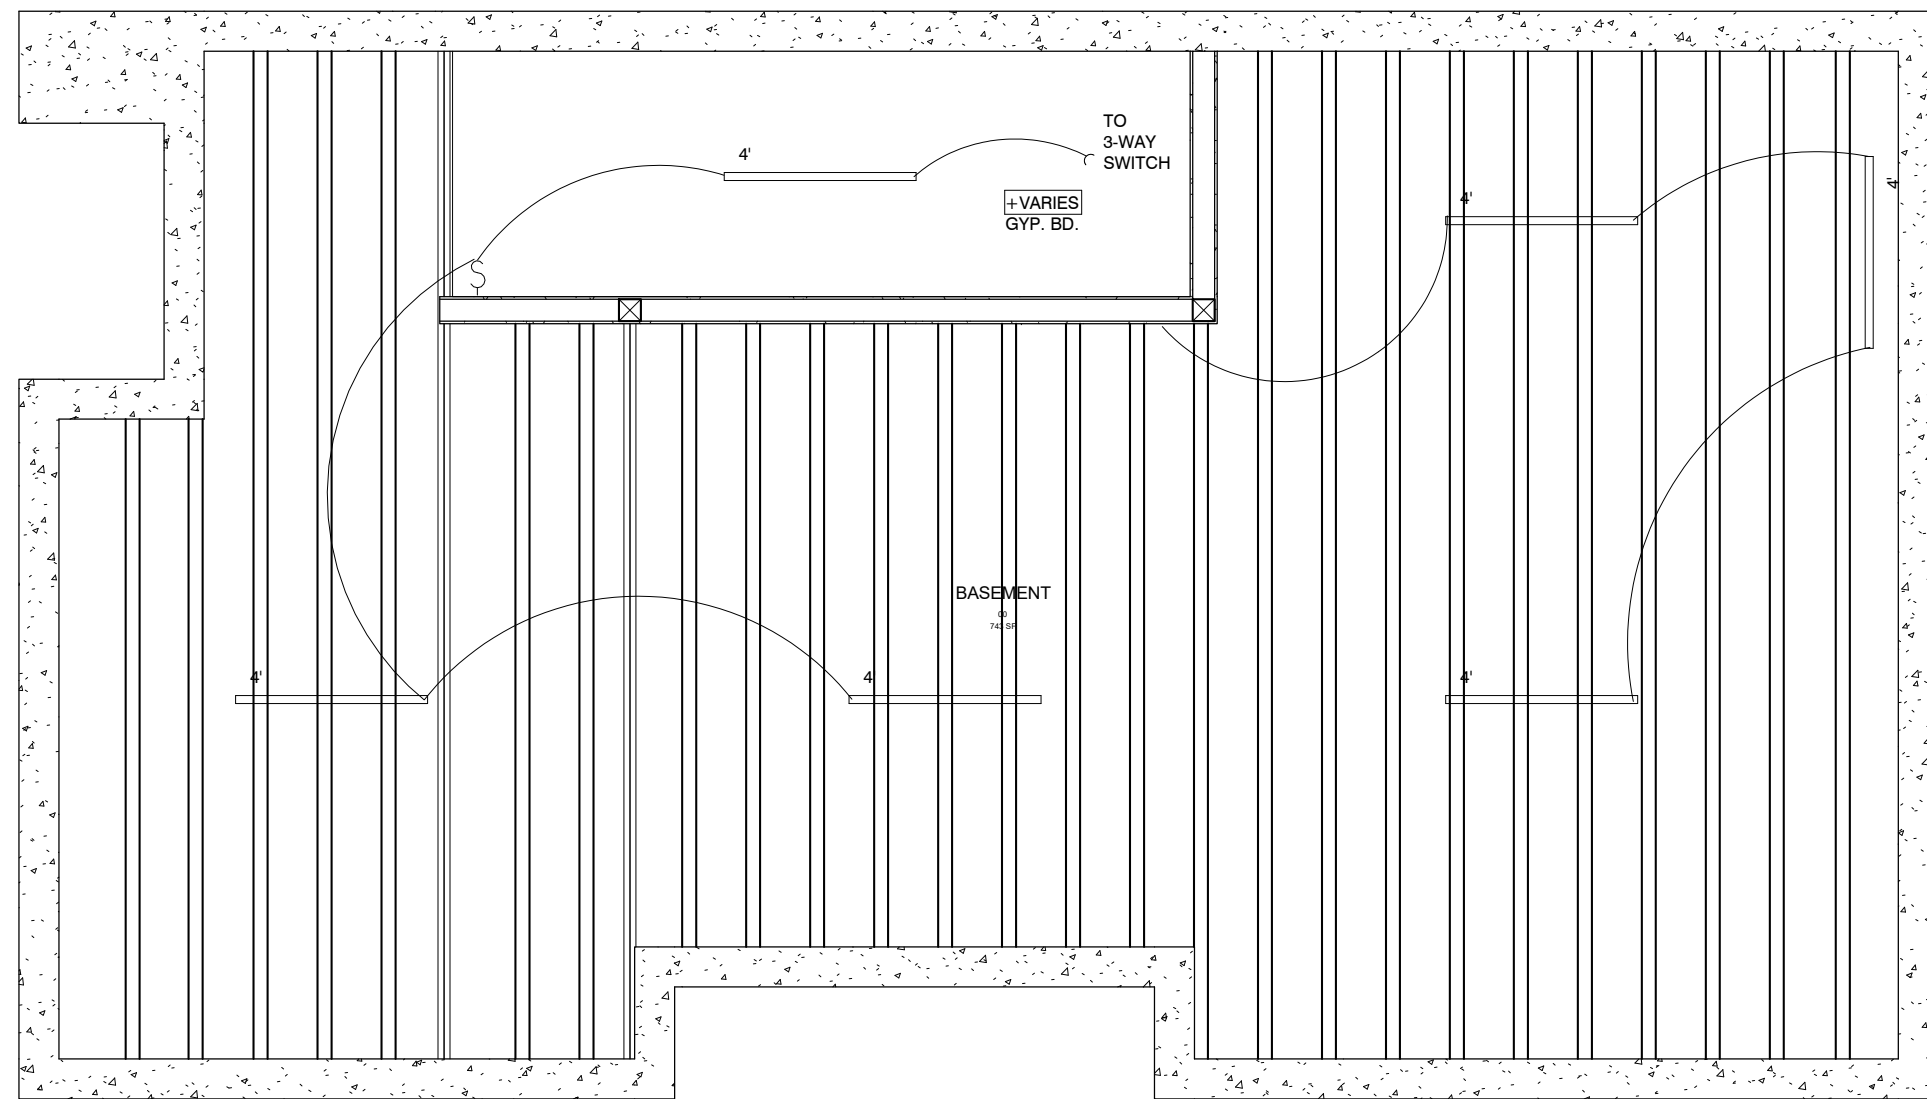

1 BASEMENT LIGHTING PLAN
1/4" = 1'-0"

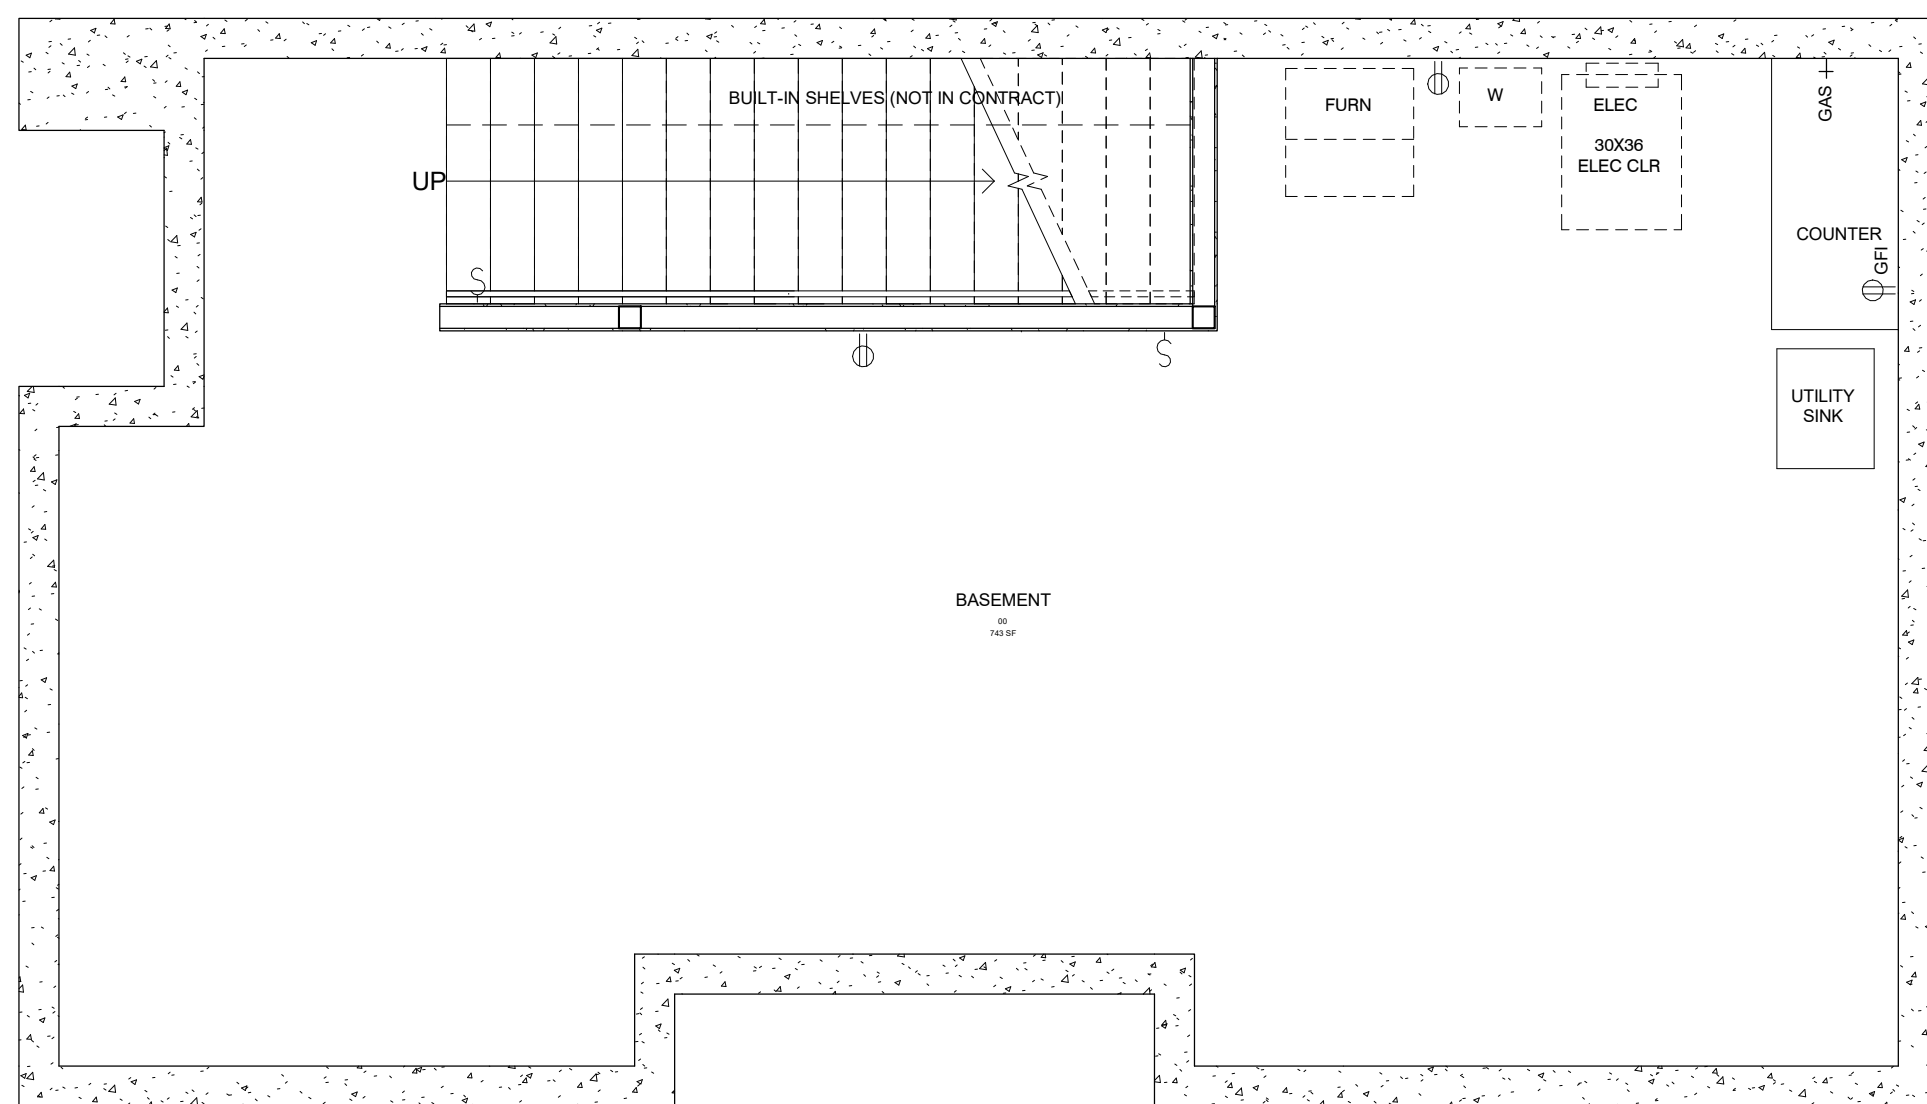

② BASEMENT POWER PLAN
1/4" = 1'-0"

ELECTRICAL SYSTEMS SHALL BE DESIGN-BUILT ON SITE BY SUB-CONTRACTOR. DRAWINGS, INSPECTIONS, AND REQUIRED CALCULATIONS SHALL BE PROVIDED DURING CONSTRUCTION.

THESE DRAWINGS ARE NOT TO BE USED FOR CONSTRUCTION, BUT ONLY REFERENCE
OF ARCHITECTS INTENT. ALL TRADES TO COORDINATE ALL WORK WITH MECHANICAL,
ELECTRICAL, PLUMBING, ETC.

01 ALL ELECTRICAL OUTLET RECEPTACLES SHALL BE 14" OR 44" A.F.F. UNLESS OTHERWISE NOTED.

02 ALL ELECTRICAL SWITCHES SHALL BE 44" A.F.F. UNLESS OTHERWISE NOTED.

03 ALL BEDROOM CIRCUITS SHALL BE ARC FAULT PROTECTED

04 ALL MECHANICAL DUCTWORK SHALL BE RIGID

05 ALL EXTERIOR FLASHING, VENT COVERS, AND PIPES SHALL BE BLACK.

LED 2, 3, 4

SURFACE MOUNTED PENDANT LIGHT FIXTURE

SURFACE MOUNTED STRIP L.E.D., (LENGTH INDICATED BY # IN FEET)

4" RECESSED L.E.D.DOWNLIGHT

L.E.D. SURFACE MOUNT EXTERIOR GRADE WALL
SCONCE

DUPLUX RECEPTACLE

§ T. D. P. 3



SWITCH
(TIMER, DIMMER, PLUG, 3-WAY)

SURFACE MOUNTED CEILING FAN, (FIXTURE PROVIDED BY OWNER)

VENTILATION FAN