
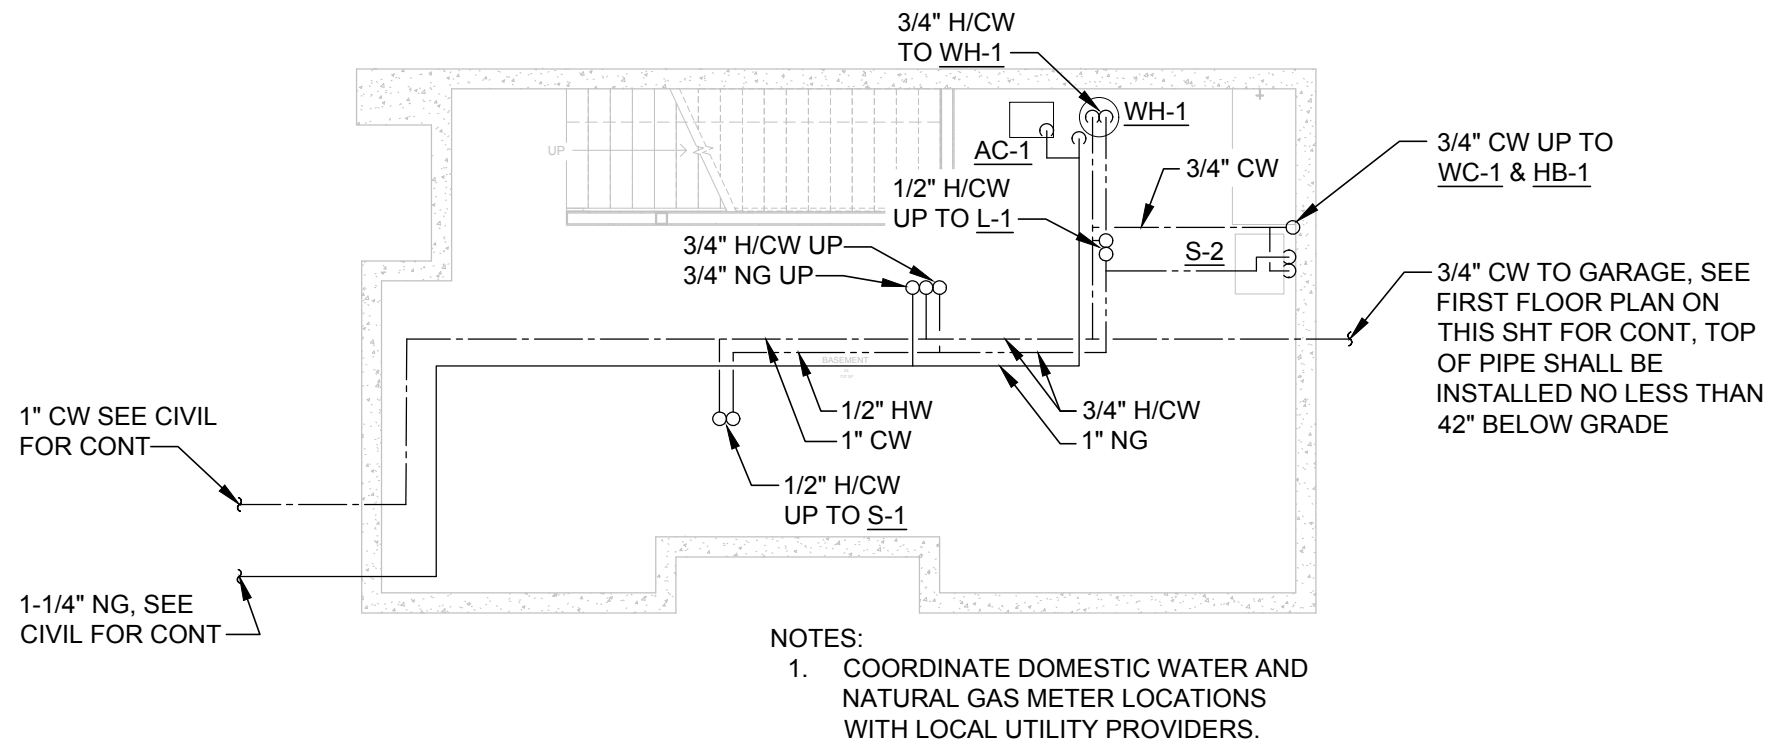
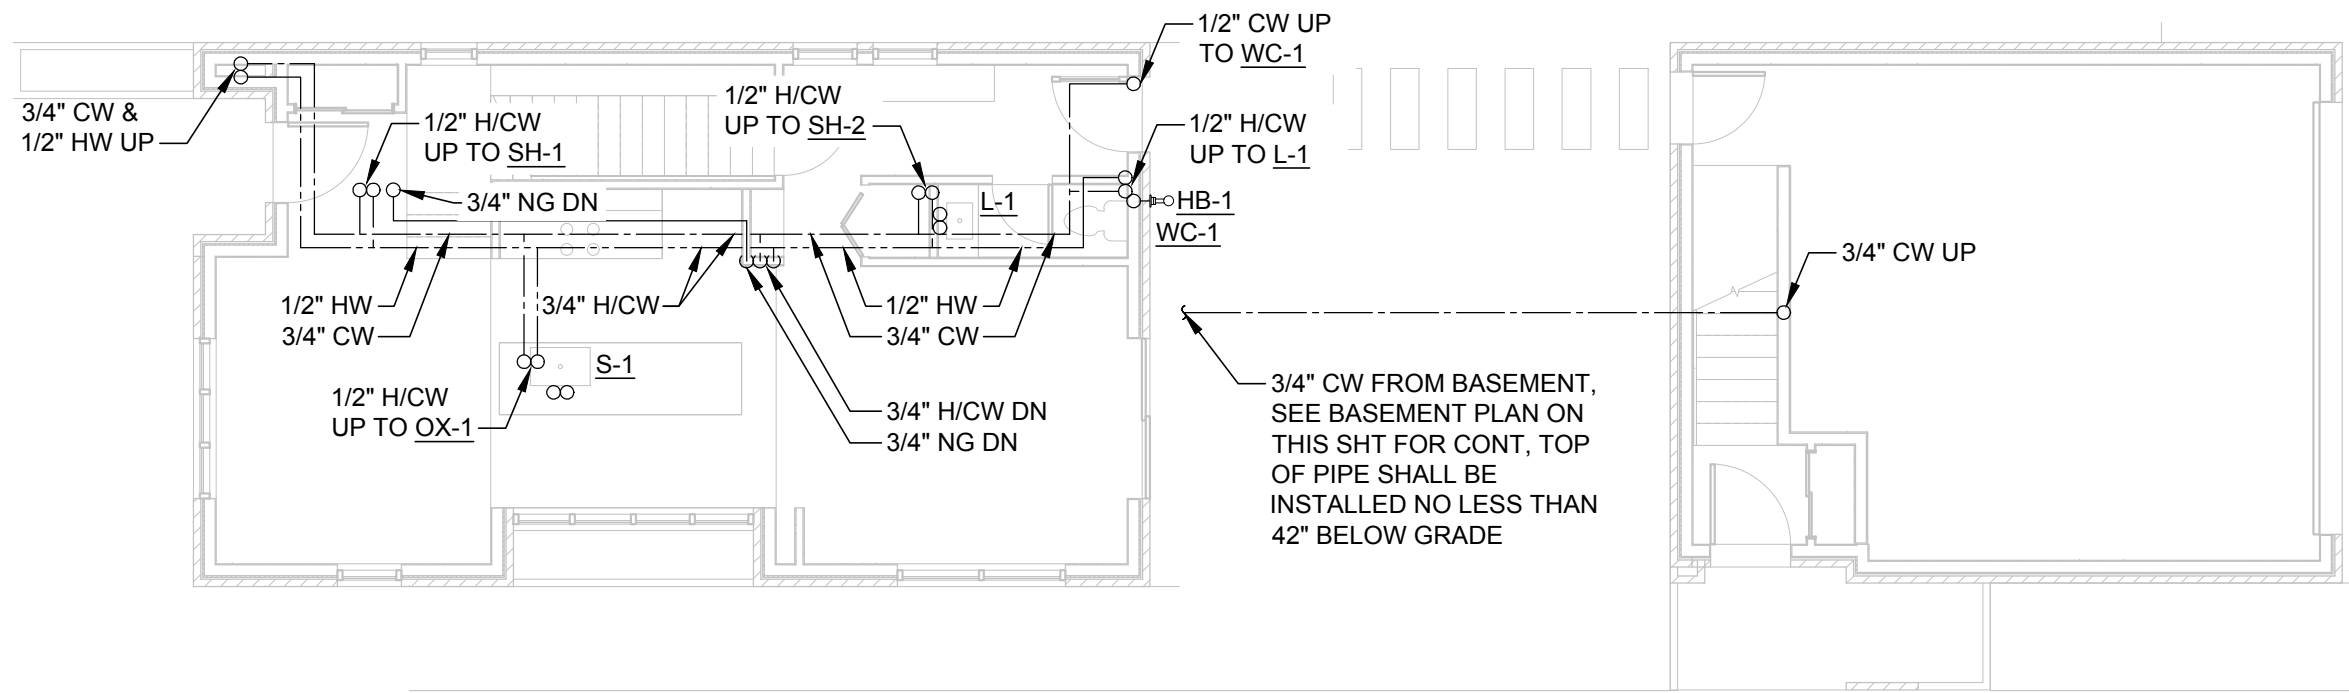


PLUMBING FIXTURE SCHEDULE	
MARK	DESCRIPTION
WC-1	FLOOR MOUNTED ADA VITREOUS CHINA ELONGATED 1.28 FLUSH GALLON CLOSE COUPLED TWO PIECE SIPHON JET WATER CLOSET, FLUSH TANK WITH 12" ROUGH-IN. AMERICAN STANDARD CLEAN WHITE MODEL #2514101S.020 OR EQUAL. PROVIDE SUPPLY & STOP. PROVIDE CLOSED FRONT SEAT. ZURN #Z5958SS-EL OR EQUAL.
L-1	LAVATORY, KOHLER: #K-2883-0 OR EQUAL: VITREOUS CHINA UNDER COUNTER MOUNT LAVATORY, SINGLE FAUCE HOLE, OVERFLOW DRAIN; FAUCET: GROHE 23589001, WITH RP330 POLISHED CHROME AERATOR; LESS POP-UP DRAIN AND LIFT HOLE IN POLISHED CHROME, 1-1/4" TAILPIECE, PROVIDE 3/8" WALL SUPPLIES WITH GRID STRAINER, P-TRAP, ADA TRAP, STOP AND SUPPLY PROTECTORS. ALT: FURNISH AND INSTALL "LAVGUARD" #102 TRAP WRAP BY TRUEBRO FOR PF-2H. TRUEBRO TEL: (800) 340-5969. INSTALL WITH AIR ADMITTANCE VALVE.
S-1	STAINLESS STEEL SINK, VIGO: #VG3019BK1, 30"X19", 10" DEEP, WITH 0 RAD. CORNERS, 3/4 HP FOOD WASTE INSINKERATOR. FAUCET: VIGO VG02001 HIGH-ARC GOOSE NECK FAUCET WITH SINGLE HANDLE AND AERATOR, OVERALL HEIGHT 18-1/2". FURNISH AND INSTALL "BROCAR" #C500R-B TRAP WRAP FOR PF6. BROCAR TEL: (800) 827-1207. INSTALL WITH AIR ADMITTANCE VALVE.
S-2	UTILITY LAUNDRY TUB W/ TRAY MUSTEE CAT. #14, 20 GAL. CAPACITY, 25"Lx23"W, ONE PIECE MOLDED CONSTRUCTION, SUPPORT WITH LEGS AT 30" A.F.F. TO LIP OF SINK, FAUCET: 93.600 POLISHED CHROME FINISH, BRASS WATERWAYS, 4" CENTER, 6" HIGH RISE TUBULAR SWING SPOUT WITH AERATOR, LEVER HANDLE, 2" CAST BRASS 1" TRAP. PROVIDE 3/8" ANGLE SUPPLIES WITH STOP. INSTALL WITH AIR ADMITTANCE VALVE.
S-3	STAINLESS STEEL SINK, VIGO: #VG2318CK1, 23"X18", 10" DEEP, WITH 0 RAD. CORNERS, 3/4 HP FOOD WASTE INSINKERATOR. FAUCET: VIGO VG02001 HIGH-ARC GOOSE NECK FAUCET WITH SINGLE HANDLE AND AERATOR, OVERALL HEIGHT 18-1/2". FURNISH AND INSTALL "BROCAR" #C500R-B TRAP WRAP FOR PF6. BROCAR TEL: (800) 827-1207. INSTALL WITH AIR ADMITTANCE VALVE.
FCO-1	FLOOR CLEAN OUT. SIZE & INSTALL AS SHOWN ON PLANS. JOSAM, ZURN OR EQUAL.
FD-1	FLOOR, ZURN #FD-2290 OR EQUAL, CAST IRON BODY, CLAMP COLLAR AND ADJUSTABLE 3" NICKEL BRONZE STRAINER ASSEMBLY. INSTALL WITH TP-1.
TP-1	AUTOMATIC TRAP PRIMER. PRECISION PLUMBING PRODUCTS PR-500
SH-1	SHOWER VALVE, GROHE CONCETTO 3507310A, SINGLE HANDLE PRESSURE BALANCING MIXING SHOWER VALVE, WITH SINGLE BRONZE STEM, STAINLESS STEEL BALANCING PISTON INTEGRAL WITH STEM ASSEMBLY, METAL LEVER HANDLE, INTEGRAL SERVICE STOPS ANS BRASS ADJUSTMENT LIMIT STOP SCREW IN CAP. EXPOSED TRIM WITH POLISHED NICKEL CHROME PLATED SURFACE. VALVE SUPPLIED WITH WALL SHOWER HEAD; PROVIDE WITH SHOWER DRAIN, ZURN MODEL Z415BZ.
SH-2	SHOWER VALVE, GROHE CONCETTO 3507510A, SINGLE HANDLE PRESSURE BALANCING MIXING SHOWER VALVE, WITH SINGLE BRONZE STEM, STAINLESS STEEL BALANCING PISTON INTEGRAL WITH STEM ASSEMBLY, METAL LEVER HANDLE, INTEGRAL SERVICE STOPS ANS BRASS ADJUSTMENT LIMIT STOP SCREW IN CAP. EXPOSED TRIM WITH POLISHED NICKEL CHROME PLATED SURFACE. VALVE SUPPLIED WITH WALL SHOWER HEAD; PROVIDE WITH SHOWER DRAIN, ZURN MODEL Z415BZ.
OX-1	OX BOX: WASHING MACHINE OUTLET BOX, SIOUX CHIEF MODEL 696-2303CF OR EQUIVALENT
HB-1	HOSE BIBB, WOODFORD MODEL #14 OR EQUAL.

GAS WATER HEATER SCHEDULE									
UNIT I.D.	LOCATION	STORAGE CAPACITY (GAL)	FUEL TYPE	INPUT RATE (MBH)	RECOVERY @90°F RISE	INLET TEMP °F	OUTLET TEMP °F	MODEL NO.	REMARKS
WH-1	BASEMENT	39	GAS	34	36	50	140	G6-T4034NV	

NOTES: 1. MODEL NUMBERS ARE AO SMITH WHITE UNLESS OTHERWISE NOTED.

ELECTRIC WATER HEATER SCHEDULE		
TAG	MANUFACTURER	DESCRIPTION
WH-2	RHEEM	TANKLESS ELECTRIC WATER HEATER; MODEL #RETEX-36, 18.25Hx22Wx3.5D, 208 VOLT, SINGLE PHASE. INSTALL PER MANUFACTURER RECOMMENDATIONS.

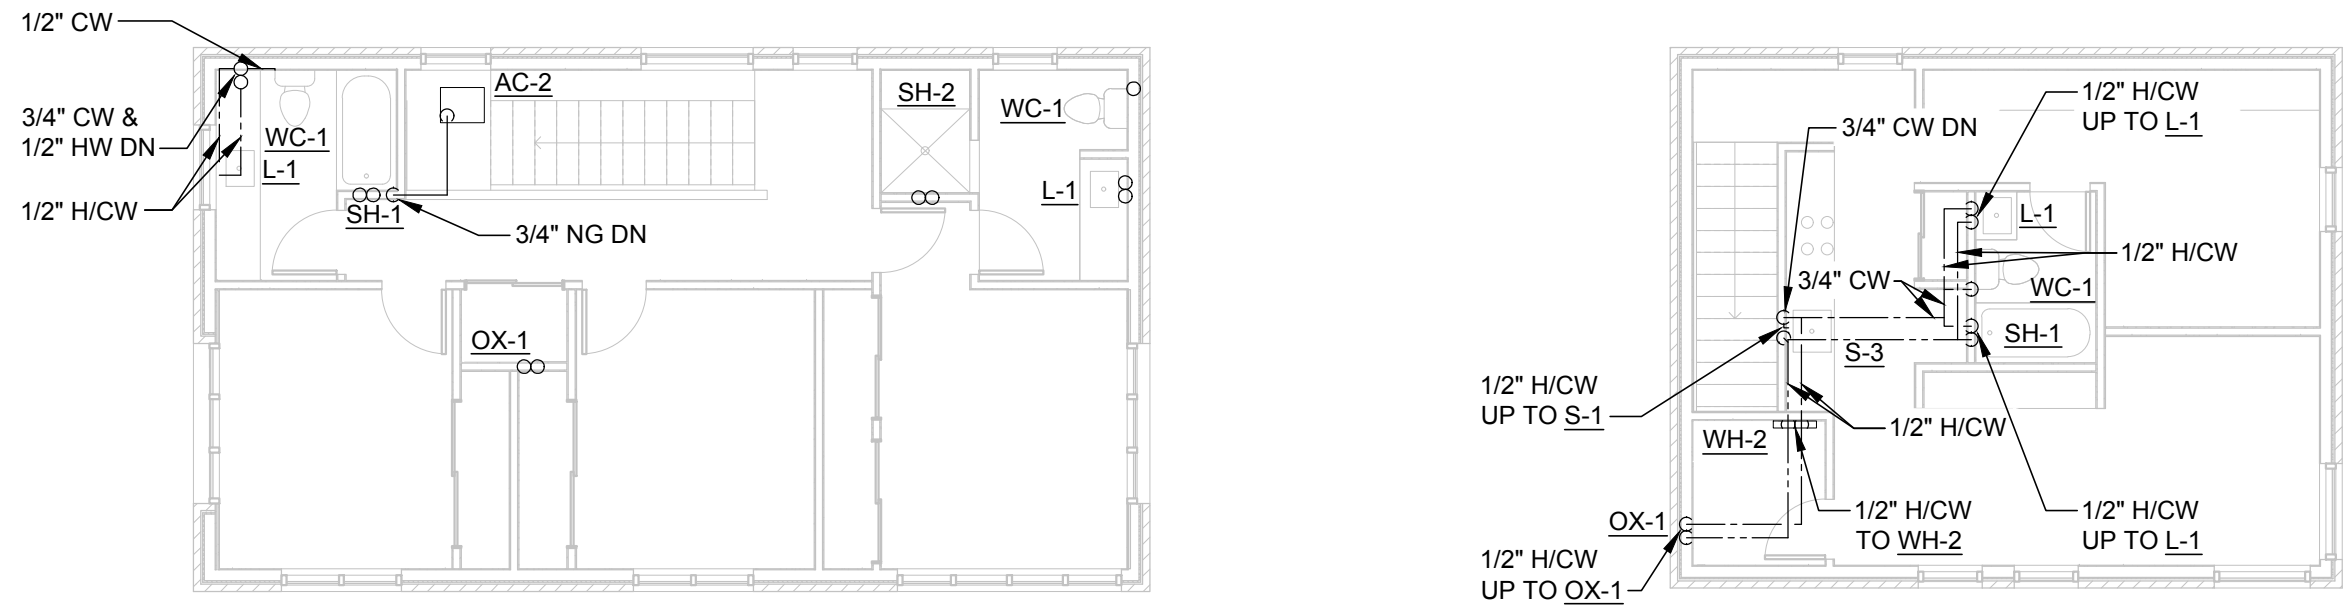

RAM MECHANICAL CONSULTING
8521 CHURCH ROAD
GROSSE ILE, MI 48138
(586) 666-1062

SEAL



THIS DRAWING SHALL NOT BE USED FOR CONSTRUCTION PURPOSES UNTIL THE SEAL AND SIGNATURE OF THE RESPONSIBLE REGISTRANT APPEARS ON THE DRAWING, AND PROPER PERMIT FORMS AND RELATED FEES ARE TRANSMITTED BY THE OWNER, OWNER'S AGENT OR CONTRACTOR TO THE AUTHORITY HAVING JURISDICTION.

CONSULTANT

CLIENT

Brian Mulloy

PROJECT

1588 Elm St.
Detroit, MI 48216

REVISIONS

06-26-2020 PERMIT

TITLE
PLUMBING
DOMESTIC WATER
FLOOR PLANS

SHEET

P2