



LM Engineering

25315 Dequindre Rd
Madison Heights, MI 48071
(248) 850-8265
LM-engineering.net

Registration Seal:



11-30-20

Client:

BIOLINIA
2060 WABASH ST.
DETROIT, MI, 48216

Project Name:

1588 ELM RESIDENCE

1588 ELM, DETROIT MI, 48216

Sheet Name:

FOUNDATION PLAN

Issued For: Date:

CLIENT REVIEW 05/12/2020

COST ESTIMATE 07/23/2020

PERMIT 11/30/2020

Drawn By: EK

Checked By: LM

Approved By: LM

Job Number:

20023

Sheet Number:


S1.00

SCE: 2406

- NOTES:
- REFER TO SHEET S0.00 FOR CONCRETE AND REINFORCING SPECIFICATION.
 - REFER TO SHEET S0.00 FOR LUMBER AND OTHER SPECIFICATIONS.
 - FS-1 INDICATES FLOOR SHEATHING. SEE SHEET S0.00 FOR MORE INFORMATION.
 - TOP OF FOOTING ELEVATION SHALL BE 8" BELOW MAIN FINISH FLOOR. FLOOR SLOPES, UNDERGROUND LINES AND UTILITIES TO BE COORDINATED WITH ARCHITECTURAL DRAWINGS AND OTHER TRADES PRIOR TO PLACEMENT OF FOOTINGS AND SLABS. REFER TO DETAIL 2/SS.00 FOR PIPE SLEEVE THROUGH FOOTING DETAILS.
 - S-1 INDICATES 4" CONCRETE SLAB W/ 6X6 W1.4XW1.4 ON 10 MIL VAPOR BARRIER OVER 4" PEA GRAVEL. REFER TO DETAIL 1/SS.00 FOR MORE INFORMATION.


WALL FOOTING SCHEDULE		
MARK	DIMENSIONS	WxD
WF8	8" x 40"	(2) #5 T&B
WF12	12" x 40"	(2) #5 T&B
WF20	20" x 40"	(3) #5 T&B
WF24	24" x 40"	(3) #5 T&B

WOOD FRAMING LEGEND	
☒	INDICATES (2) 2x6 POST UNLESS NOTED OTHERWISE
☐	POINT LOAD ABOVE

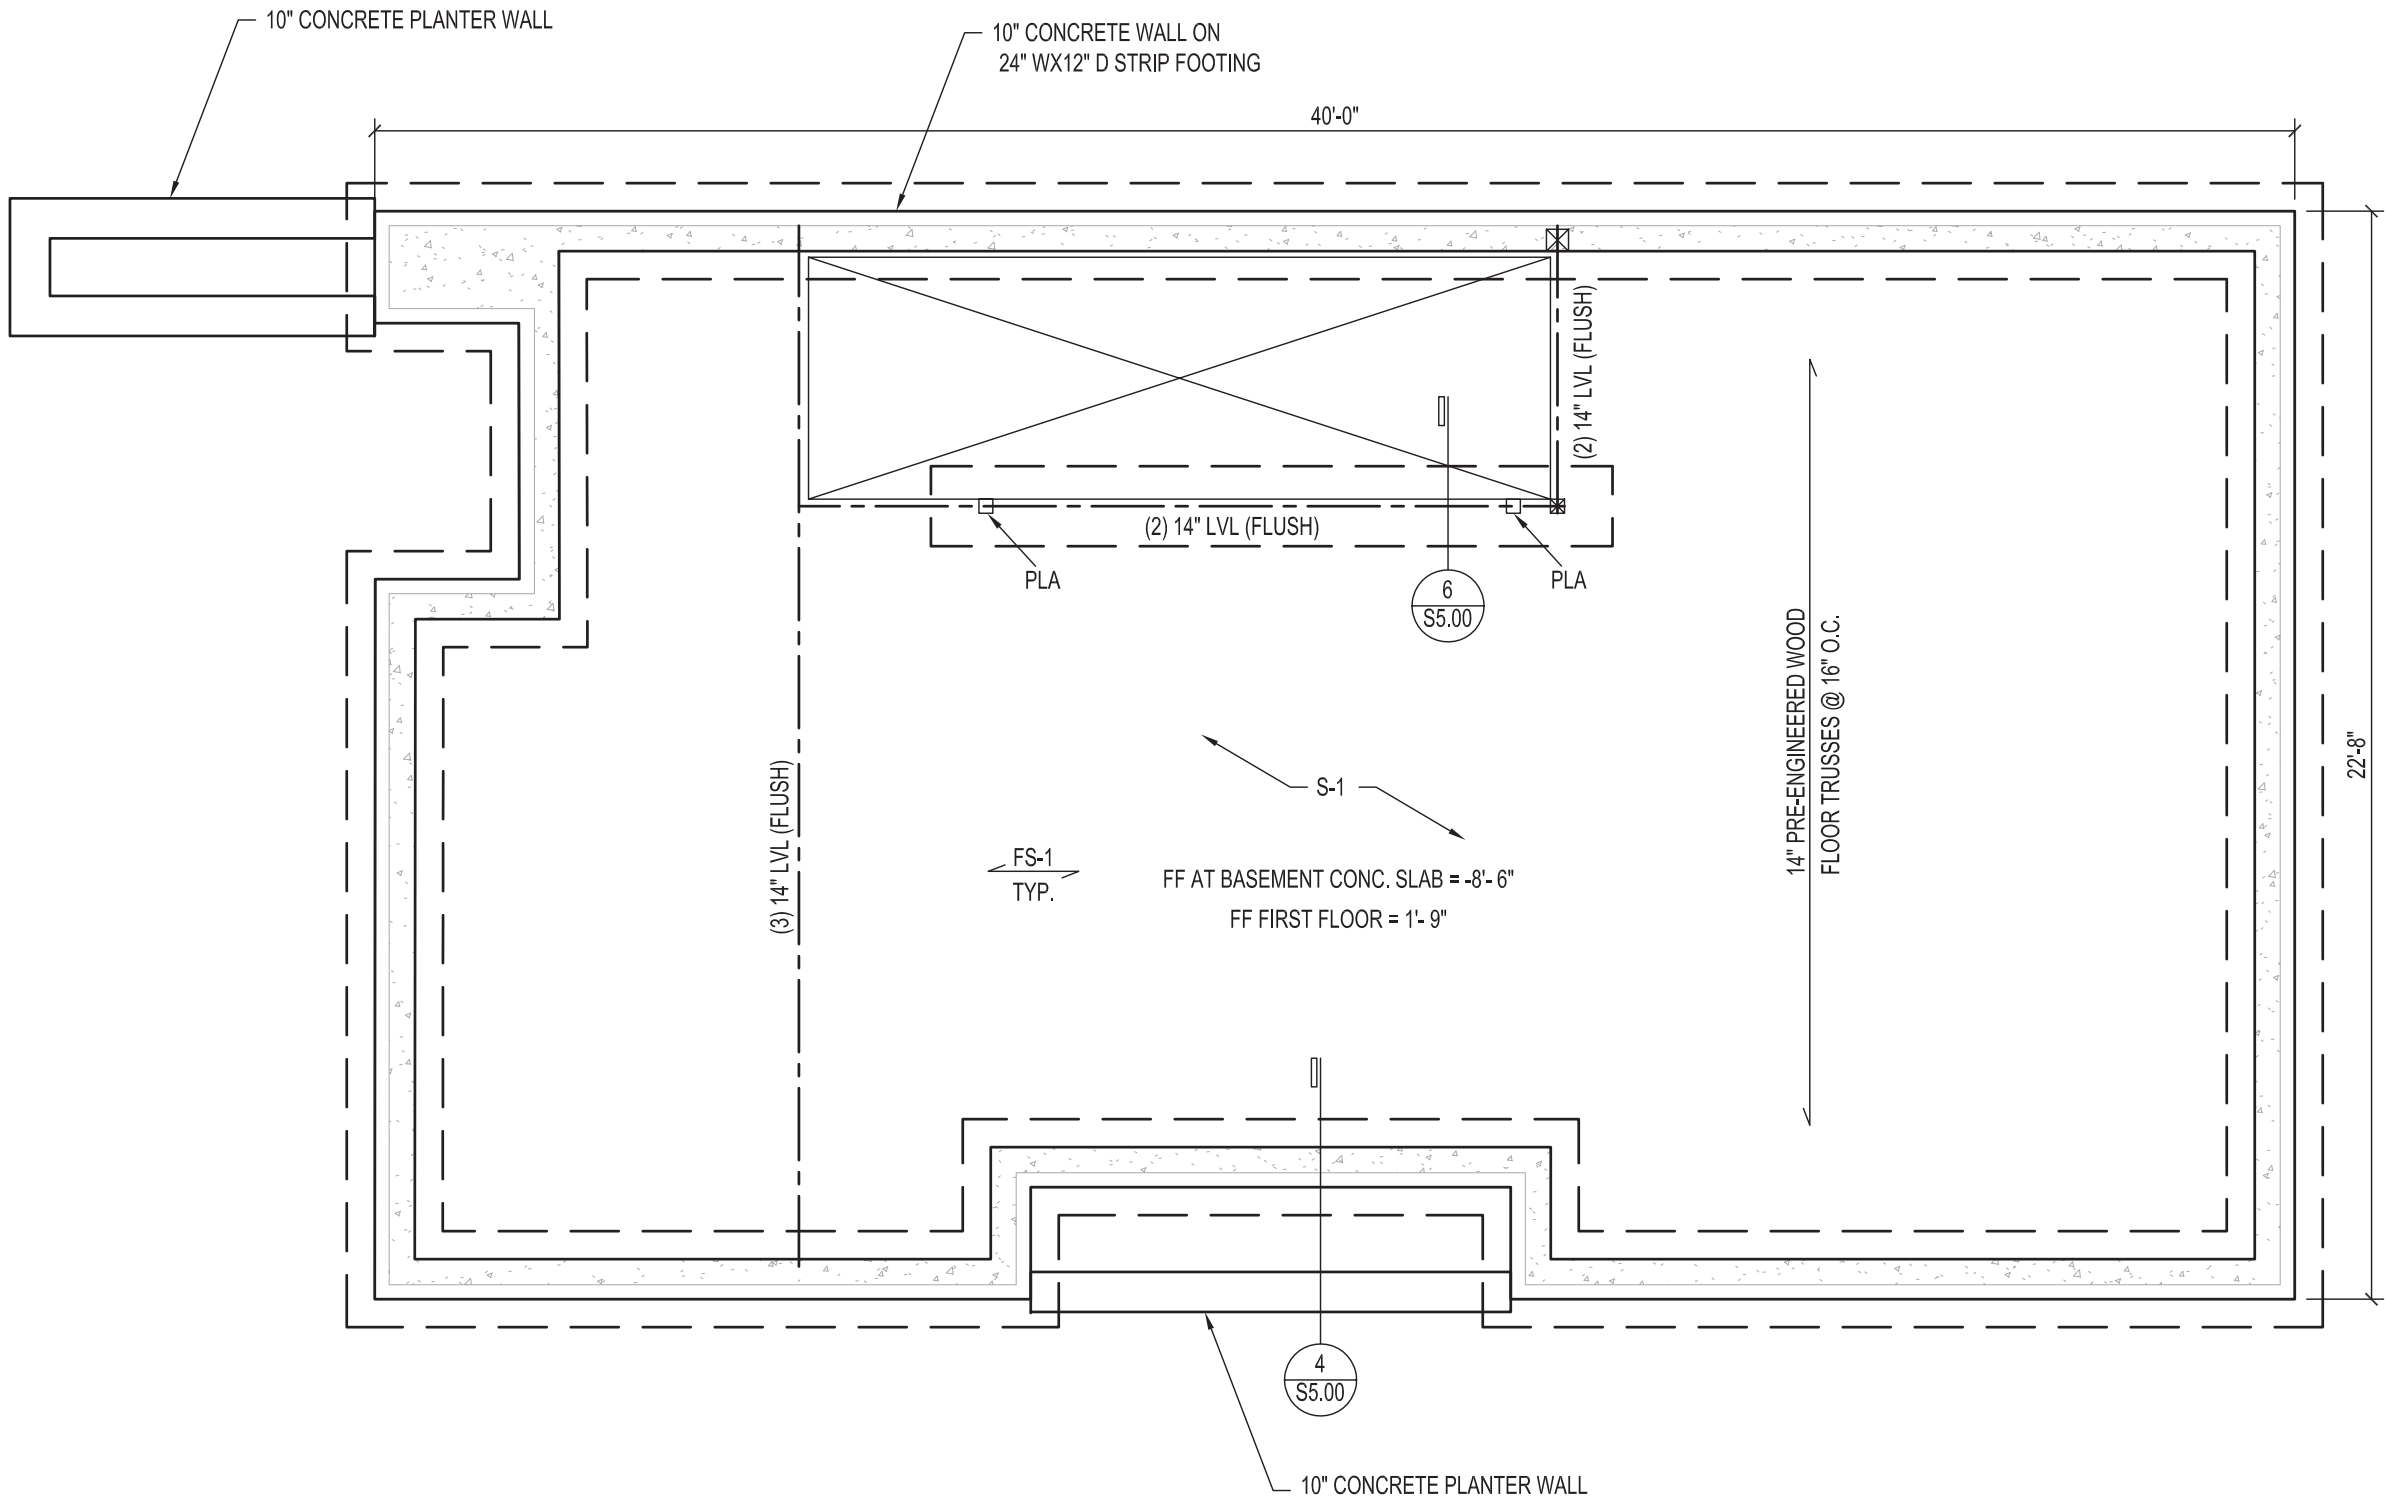

FOUNDATION PLAN & 1ST FLOOR FRAMING

SCALE: 1/4" = 1'-0"

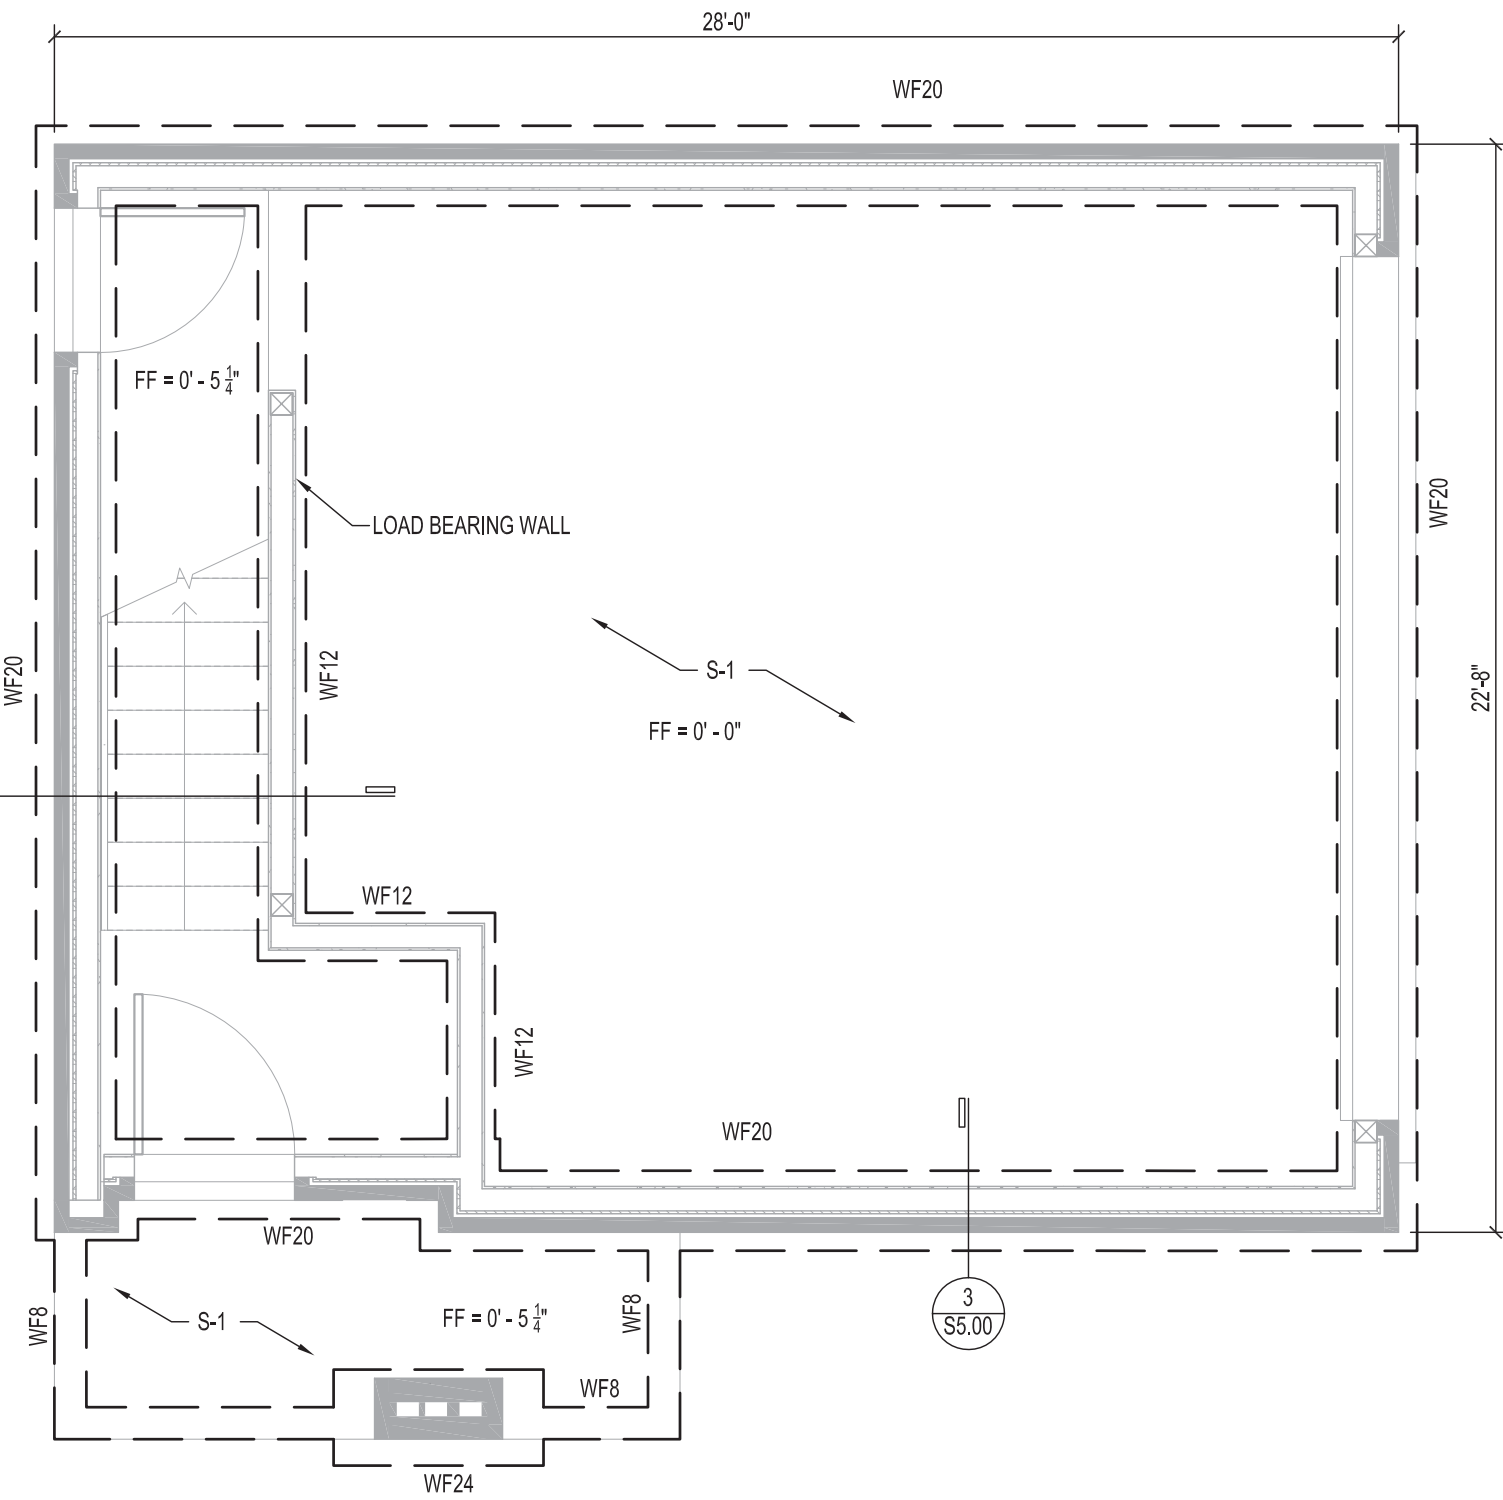

FOUNDATION PLAN

SCALE: 1/4" = 1'-0"