




**Registration Seal:**

 

Project Name:

# 1588 ELM RESIDENCE

1588 F I M DETROIT MI 48216

Sheet Name:

**SECOND FLOOR  
FRAMING PLAN**

Issued For:

|  |
|--|
|  |
|  |
|  |
|  |

Approved By: \_\_\_\_\_

Job Number:

20023


Sheet Number:

## S2.02

SIZE: 24x3

- NOTES:
1. REFER TO SHEET \$0.00 FOR LUMBER AND OTHER SPECIFICATIONS.
  2. BUILD-UP HEADERS SHALL BE ATTACHED WITH CONSTRUCTION GLUE AND GRK SCREWS AT 10" O.C. STAGGERED. BUILD-UP SHALL HAVE THE FOLLOWING CONSTRUCTION UNLESS NOTED OTHERWISE ON THE PLAN:
    - 2X4 WALL: (2) 2X10 (MIN) + 1/2" PLYWOOD (3-1/2" TOTAL WIDTH)
    - 2X6 WALL: (3) 2X10 + (2) 1/2" PLYWOOD (5-1/2" TOTAL WIDTH).
  3. ALL HEADERS SHALL HAVE A MINIMUM (2) 2X JACK STUDS AT BEARING ENDS
  4. AT HEADERS TO SUPPORT 3" RIGID FLOOR, PROVIDE 1/2x12x14" (LLV) BRIC ANGLE WITH 5/16" DIAMETER X 3-1/8" GRK SCREWS @ 16" O.C. INTO HEADER.
  - FS-1 INDICATES FLOOR SHEATHING. SEE SHEET \$0.00 FOR MORE INFORMATION.
  6. 1ST FLOOR BEARING WALLS
    - EXTERIOR WALLS: 2X6 WOOD STUDS @ 16" O.C.

| WOOD FRAMING LEGEND                                                                 |                                               |
|-------------------------------------------------------------------------------------|-----------------------------------------------|
|  | INDICATES (2) 2x6 POST UNLESS NOTED OTHERWISE |
|  | POINT LOAD ABOVE                              |

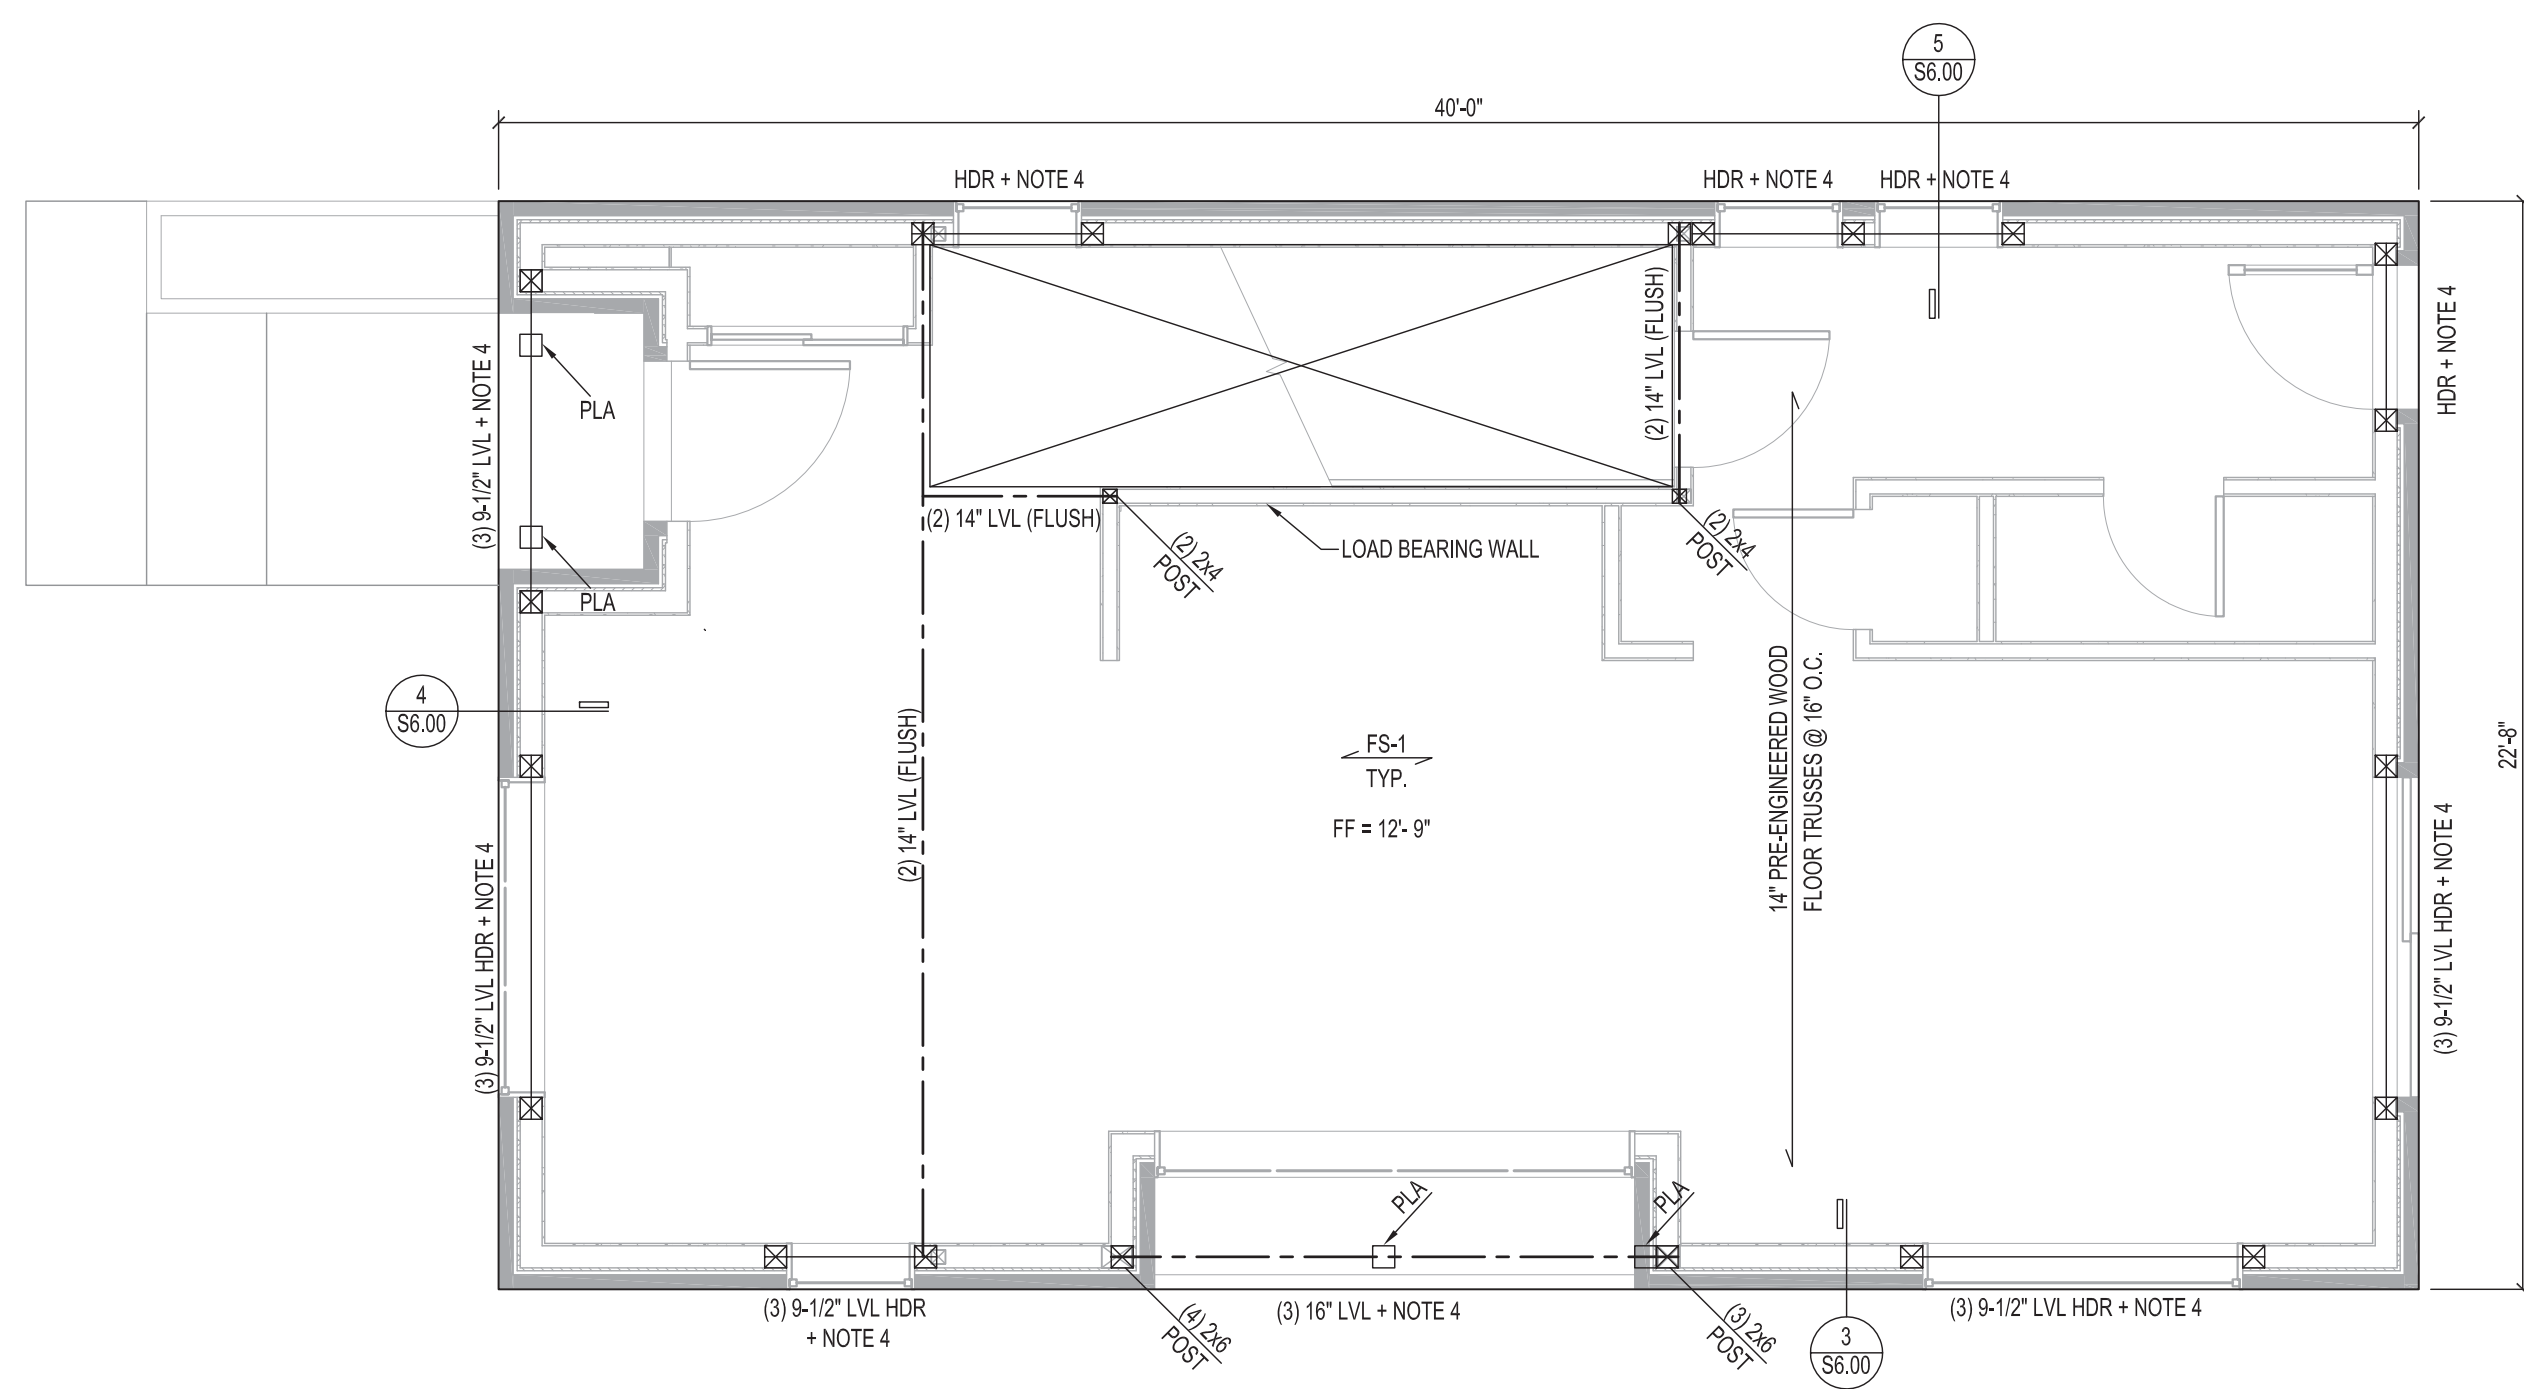

## 2ND FLOOR FRAMING PLAN

SCALE:  $1/4'' = 1'-0''$



2ND FLOOR FRAMING PLAN

SCALE:  $1/4'' = 1'-0''$

