



LM Engineering

25315 Dequindre Rd
Madison Heights, MI 48071
(248) 850-8265
LM-engineering.net

Registration Seal:



11-30-20

Client:

BIOLINIA
2060 WABASH ST.
DETROIT, MI, 48216

Project Name:

1588 ELM RESIDENCE

1588 ELM, DETROIT MI, 48216

Sheet Name:

ROOF FRAMING PLAN

Issued For: Date:

CLIENT REVIEW 05/12/2020

COST ESTIMATE 07/23/2020

PERMIT 11/30/2020

Drawn By: EK

Checked By: LM

Approved By: LM

Job Number:

20023

Sheet Number:


S3.01

SCE: 24436

NOTES:

- REFER TO SHEET S0.00 FOR LUMBER AND OTHER SPECIFICATIONS.
- BUILT-UP HEADERS SHALL BE ATTACHED WITH CONSTRUCTION GLUE AND GRK SCREWS AT 16" O.C. STAGGERED. BUILT-UP SHALL HAVE THE FOLLOWING CONSTRUCTION UNLESS NOTED OTHERWISE ON THE PLAN:
2X4 WALL: (2) 2X10 (MIN.) + 1/2" PLYWOOD (5-1/2" TOTAL WIDTH)
2X6 WALL: (3) 2X10 + (2) 1/2" PLYWOOD (5-1/2" TOTAL WIDTH).
- ALL HEADERS SHALL HAVE A MINIMUM (2) 2X JACK STUDS AT BEARING ENDS.
- AT HEADERS TO SUPPORT BRICK VENEER, PROVIDE L5x3-1/2x1/4" (LLV) BRICK ANGLE WITH 5/16" DIAMETER x 3-1/8" GRK SCREWS @ 16" O.C. INTO HEADER. RS-1 INDICATES ROOF SHEATHING SEE SHEET S0.00 FOR MORE INFORMATION.
- THE ROOF FRAMING PLAN DOES NOT ACCOUNT FOR FUTURE MECHANICAL ROOF TOP UNITS (RTU). CONTACT LME FOR DESIGN OFF RTU SUPPORT FRAMING.
- REFER TO MECHANICAL DRAWINGS FOR DRAINAGE LOCATIONS.
- 2ND FLOOR BEARING WALLS
- EXTERIOR WALLS: 2X6 WOOD STUDS @ 16" O.C.


WOOD FRAMING LEGEND	
☒	INDICATES (2) 2x6 POST UNLESS NOTED OTHERWISE

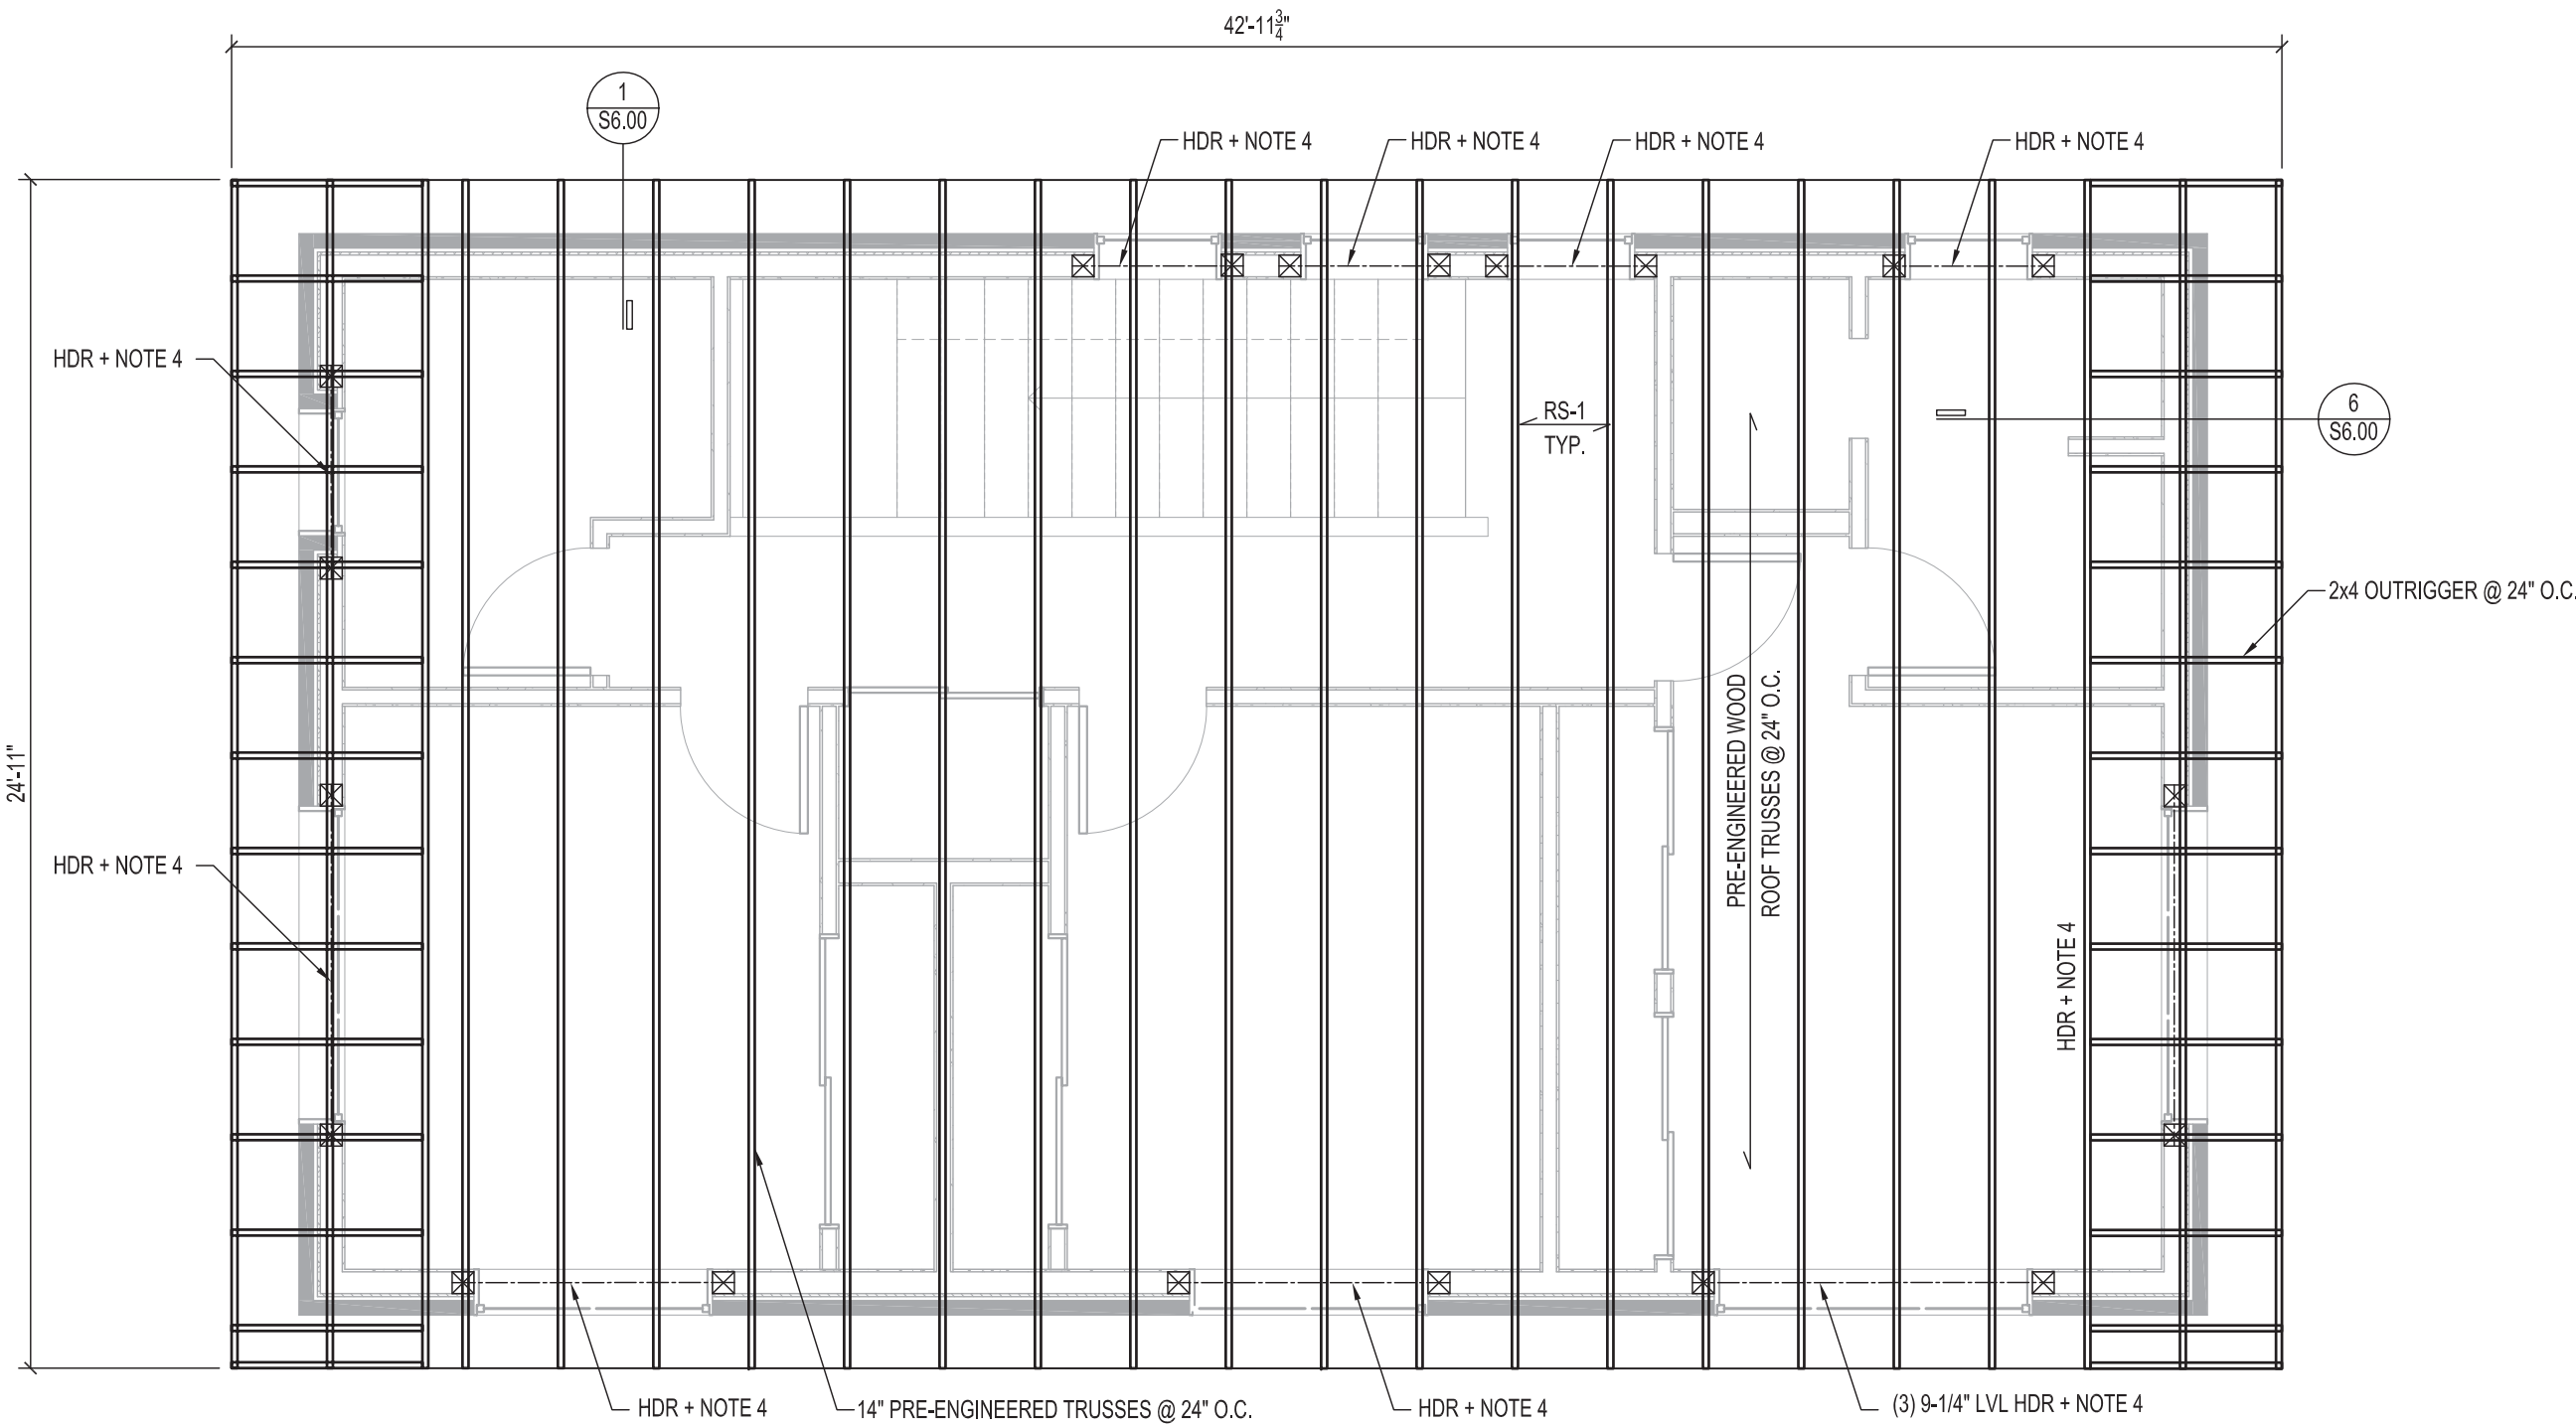

ROOF FRAMING PLAN

SCALE: 1/4" = 1'-0"

NORTH

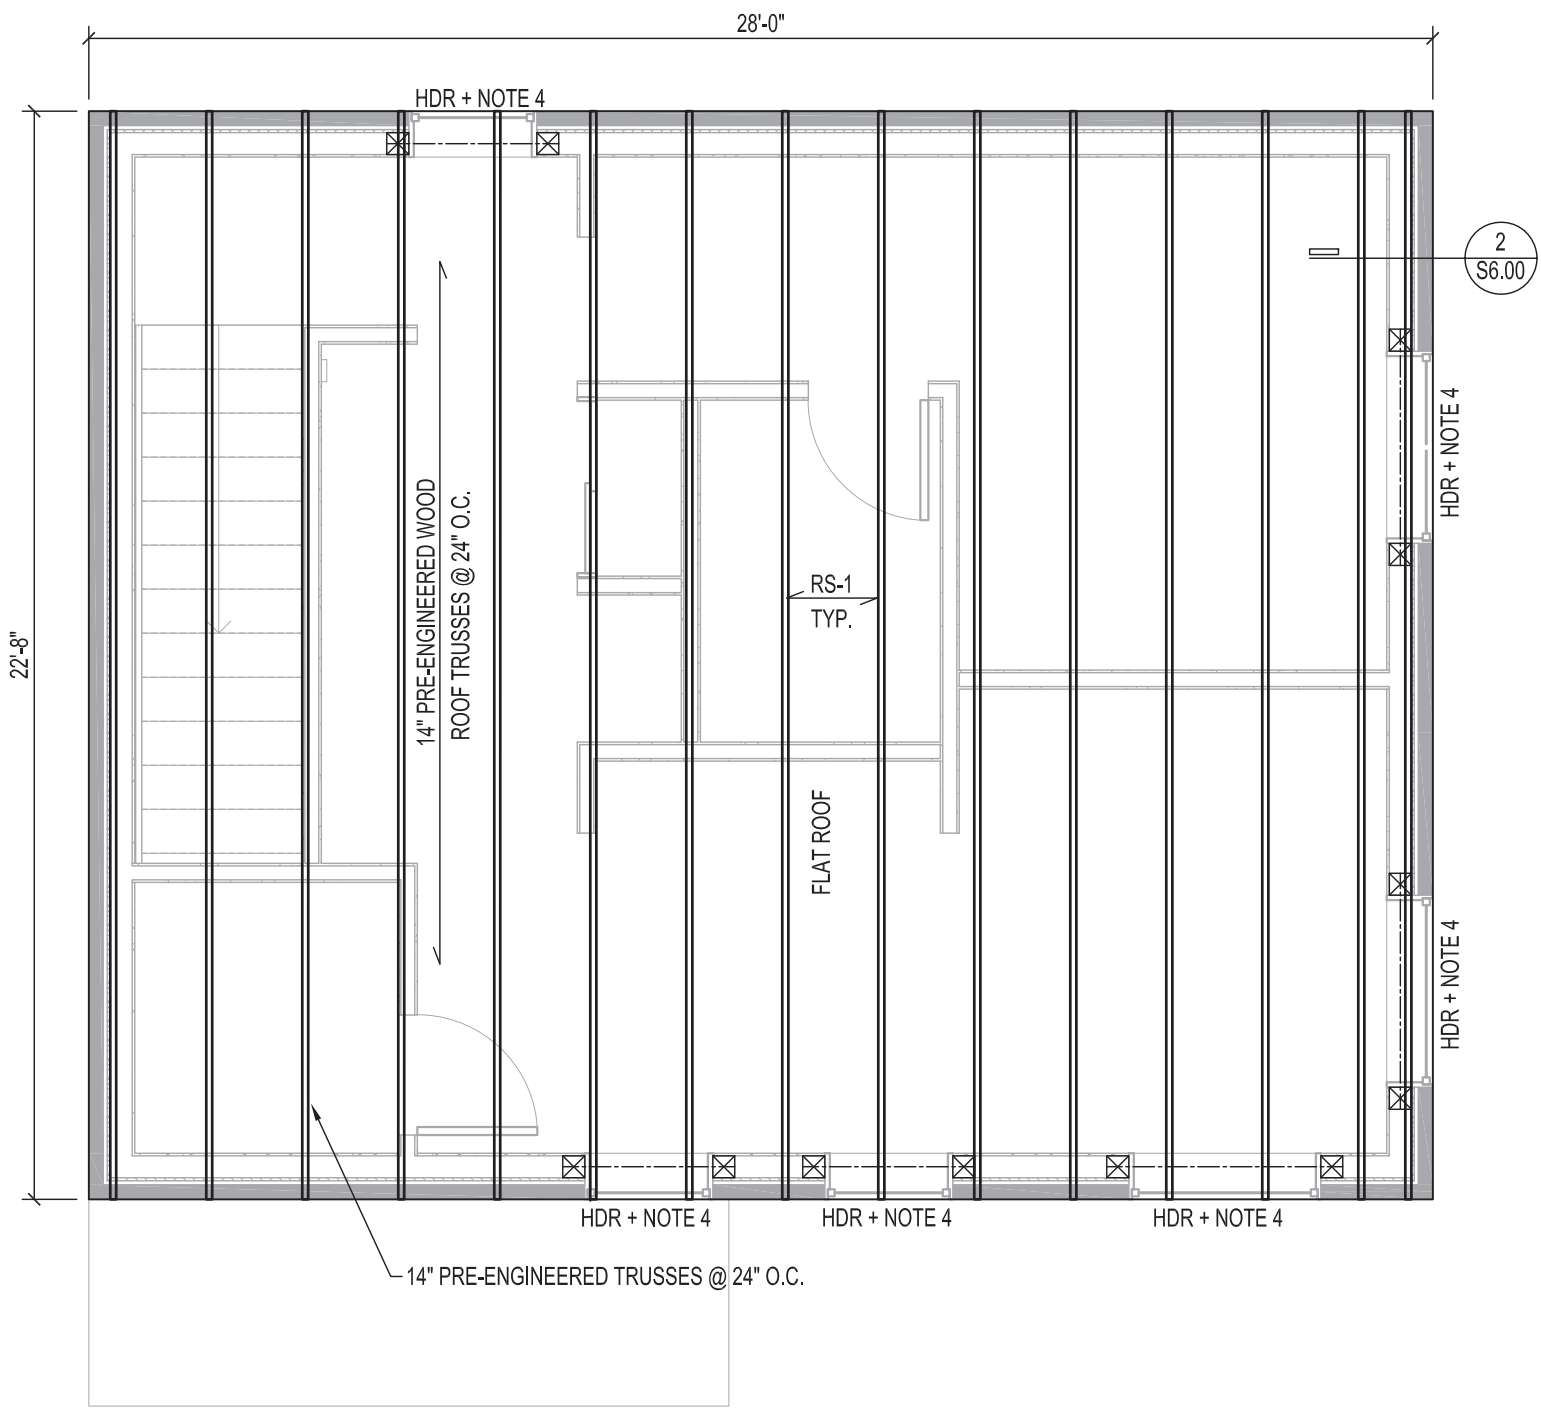

ROOF FRAMING PLAN

SCALE: 1/4" = 1'-0"

NORTH