



LM Engineering

25315 Dequindre Rd
Madison Heights, MI 48071
(248) 850-8265
LM-engineering.net

Registration Seal:



11-30-20

Client:

BIOLINIA
2060 WABASH ST.
DETROIT, MI, 48216

Project Name:

1588 ELM RESIDENCE

1588 ELM, DETROIT MI, 48216

Sheet Name:

FRAMING DETAILS

Issued For:	Date:
CLIENT REVIEW	05/12/2020
COST ESTIMATE	07/23/2020
PERMIT	11/30/2020

Drawn By:	EK
Checked By:	LM
Approved By:	LM


Job Number:

20023

Sheet Number:

S6.00


SCE: 24436

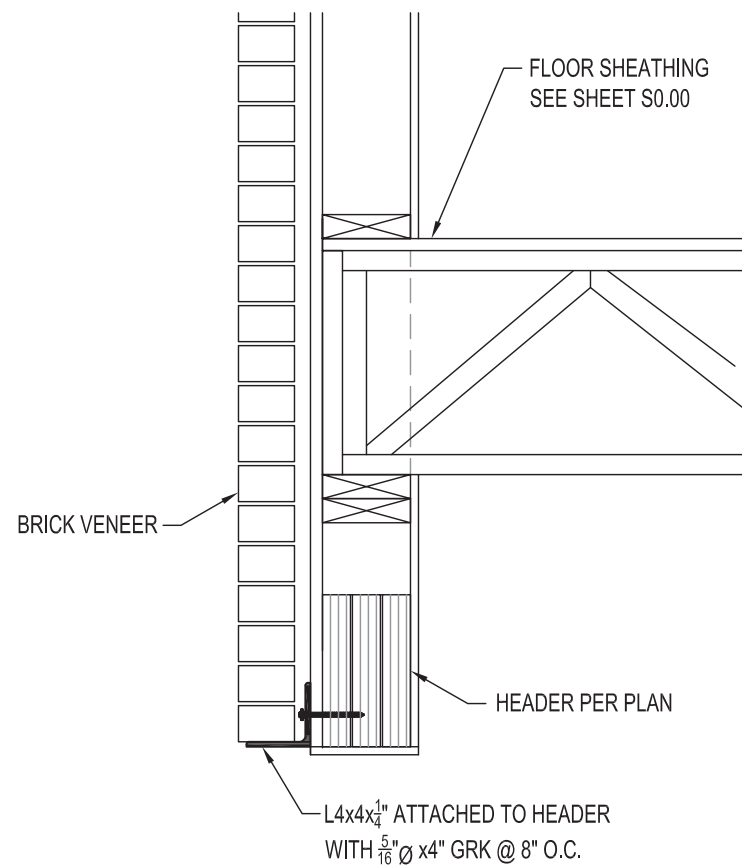

5

TYPICAL HEADER DETAIL


SCALE: 1" = 1'-0"

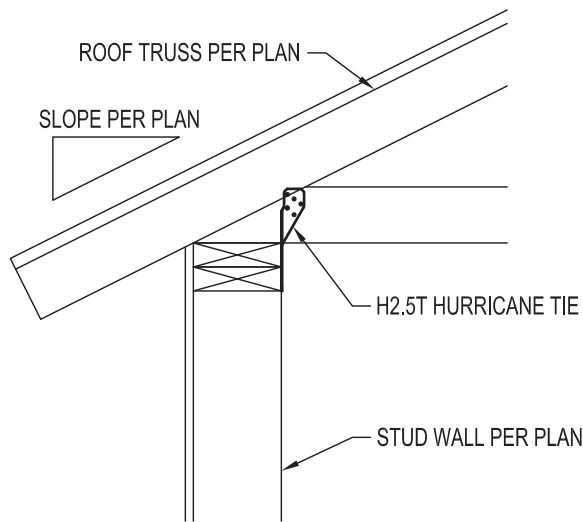

1

TYPICAL ROOF TRUSS CONNECTION


SCALE: 1" = 1'-0"

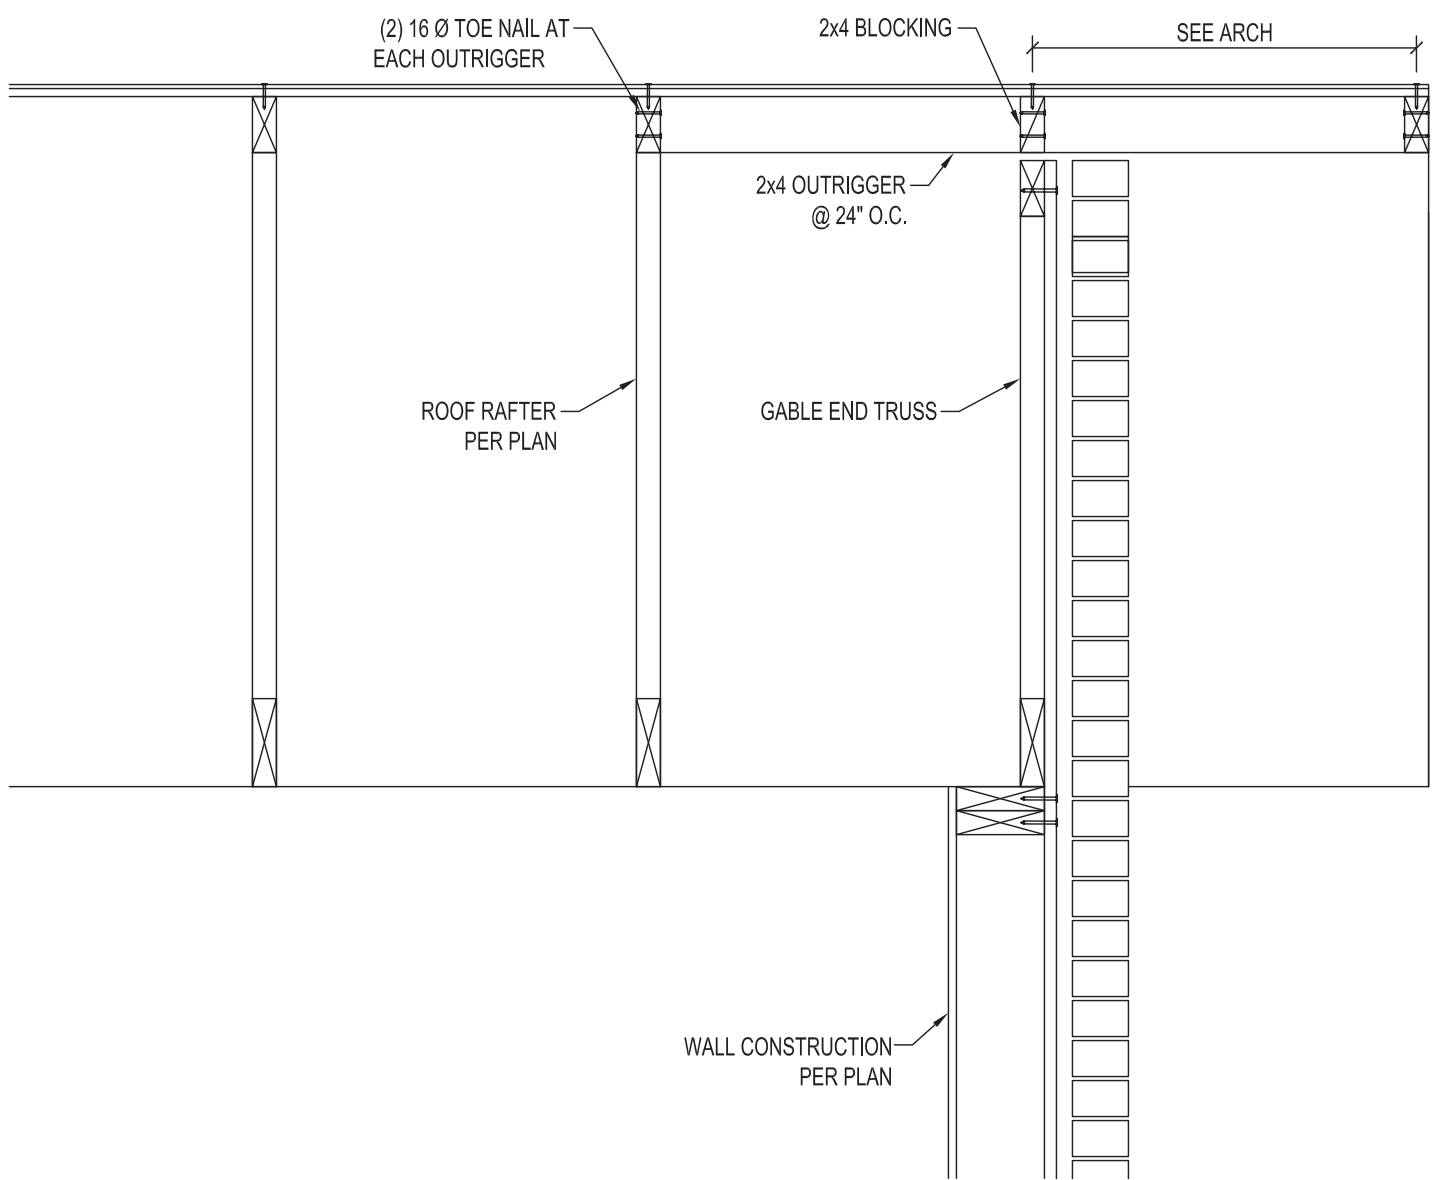

6

TYPICAL ROOF OVERHANG


SCALE: 1" = 1'-0"

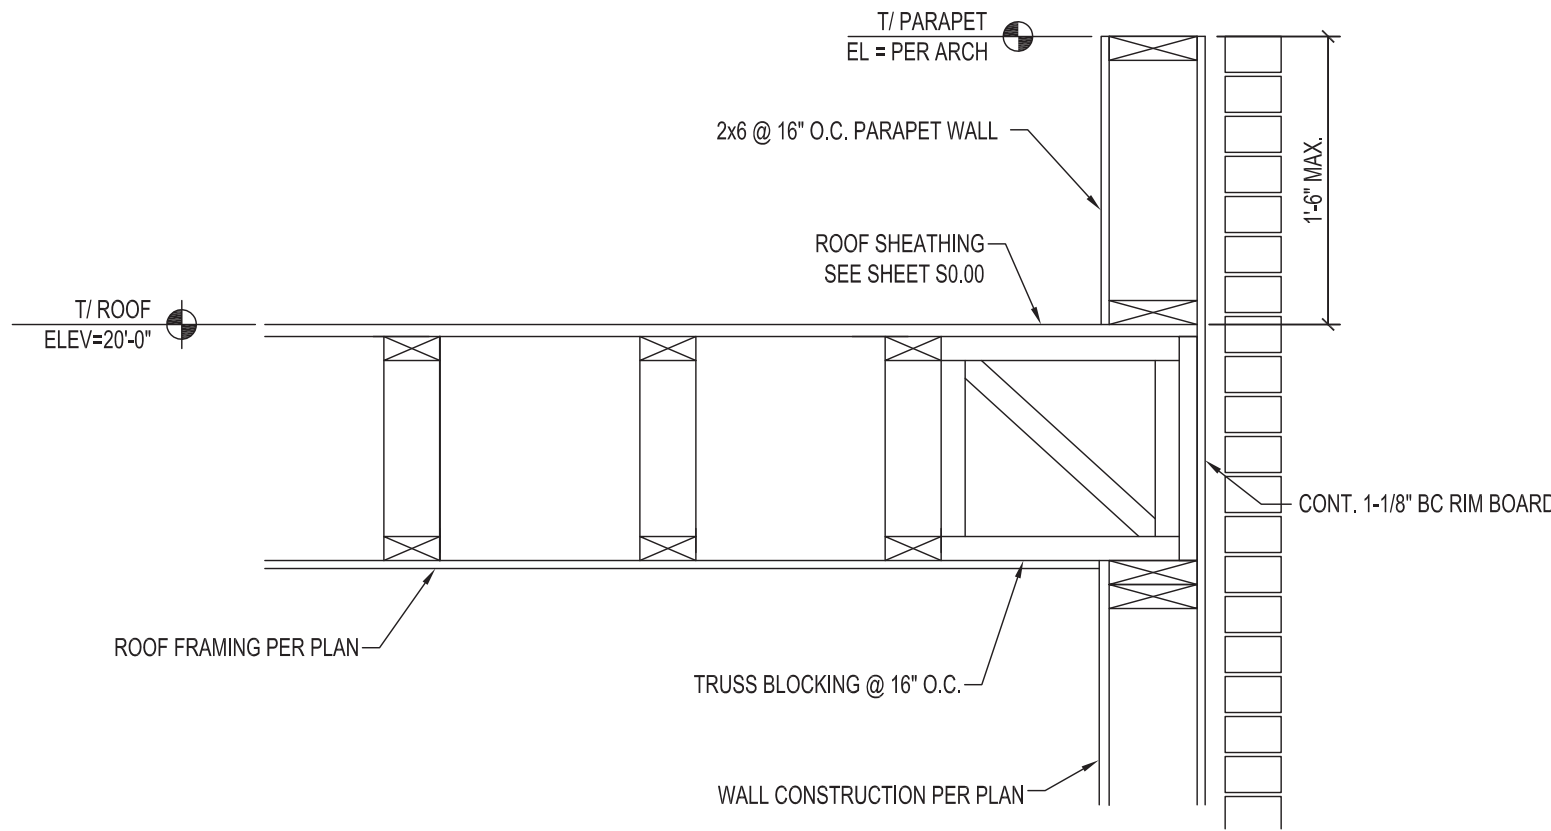

2

PARAPET SECTION


SCALE: 1" = 1'-0"

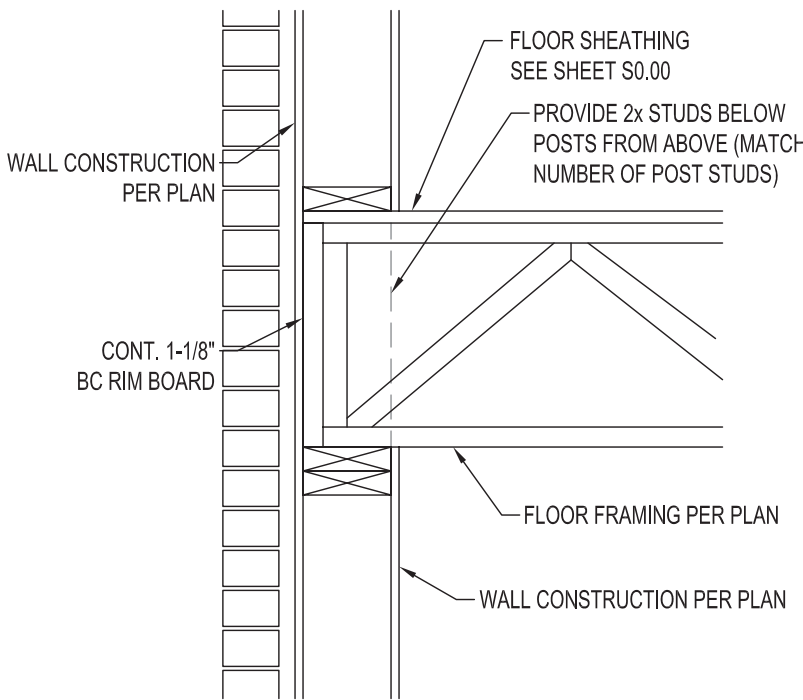

3

FRAMING SECTION

SCALE: 1" = 1'-0"

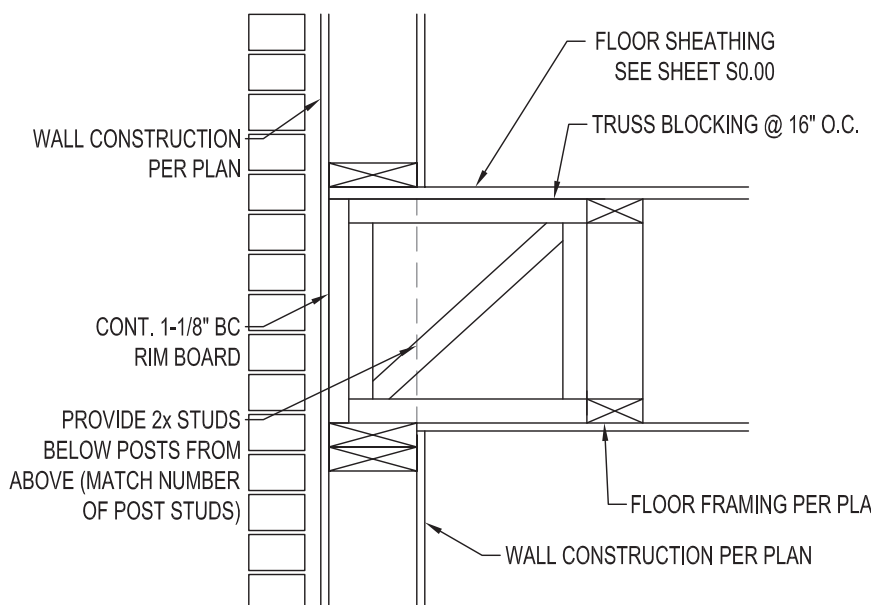

4

FRAMING SECTION

SCALE: 1" = 1'-0"